


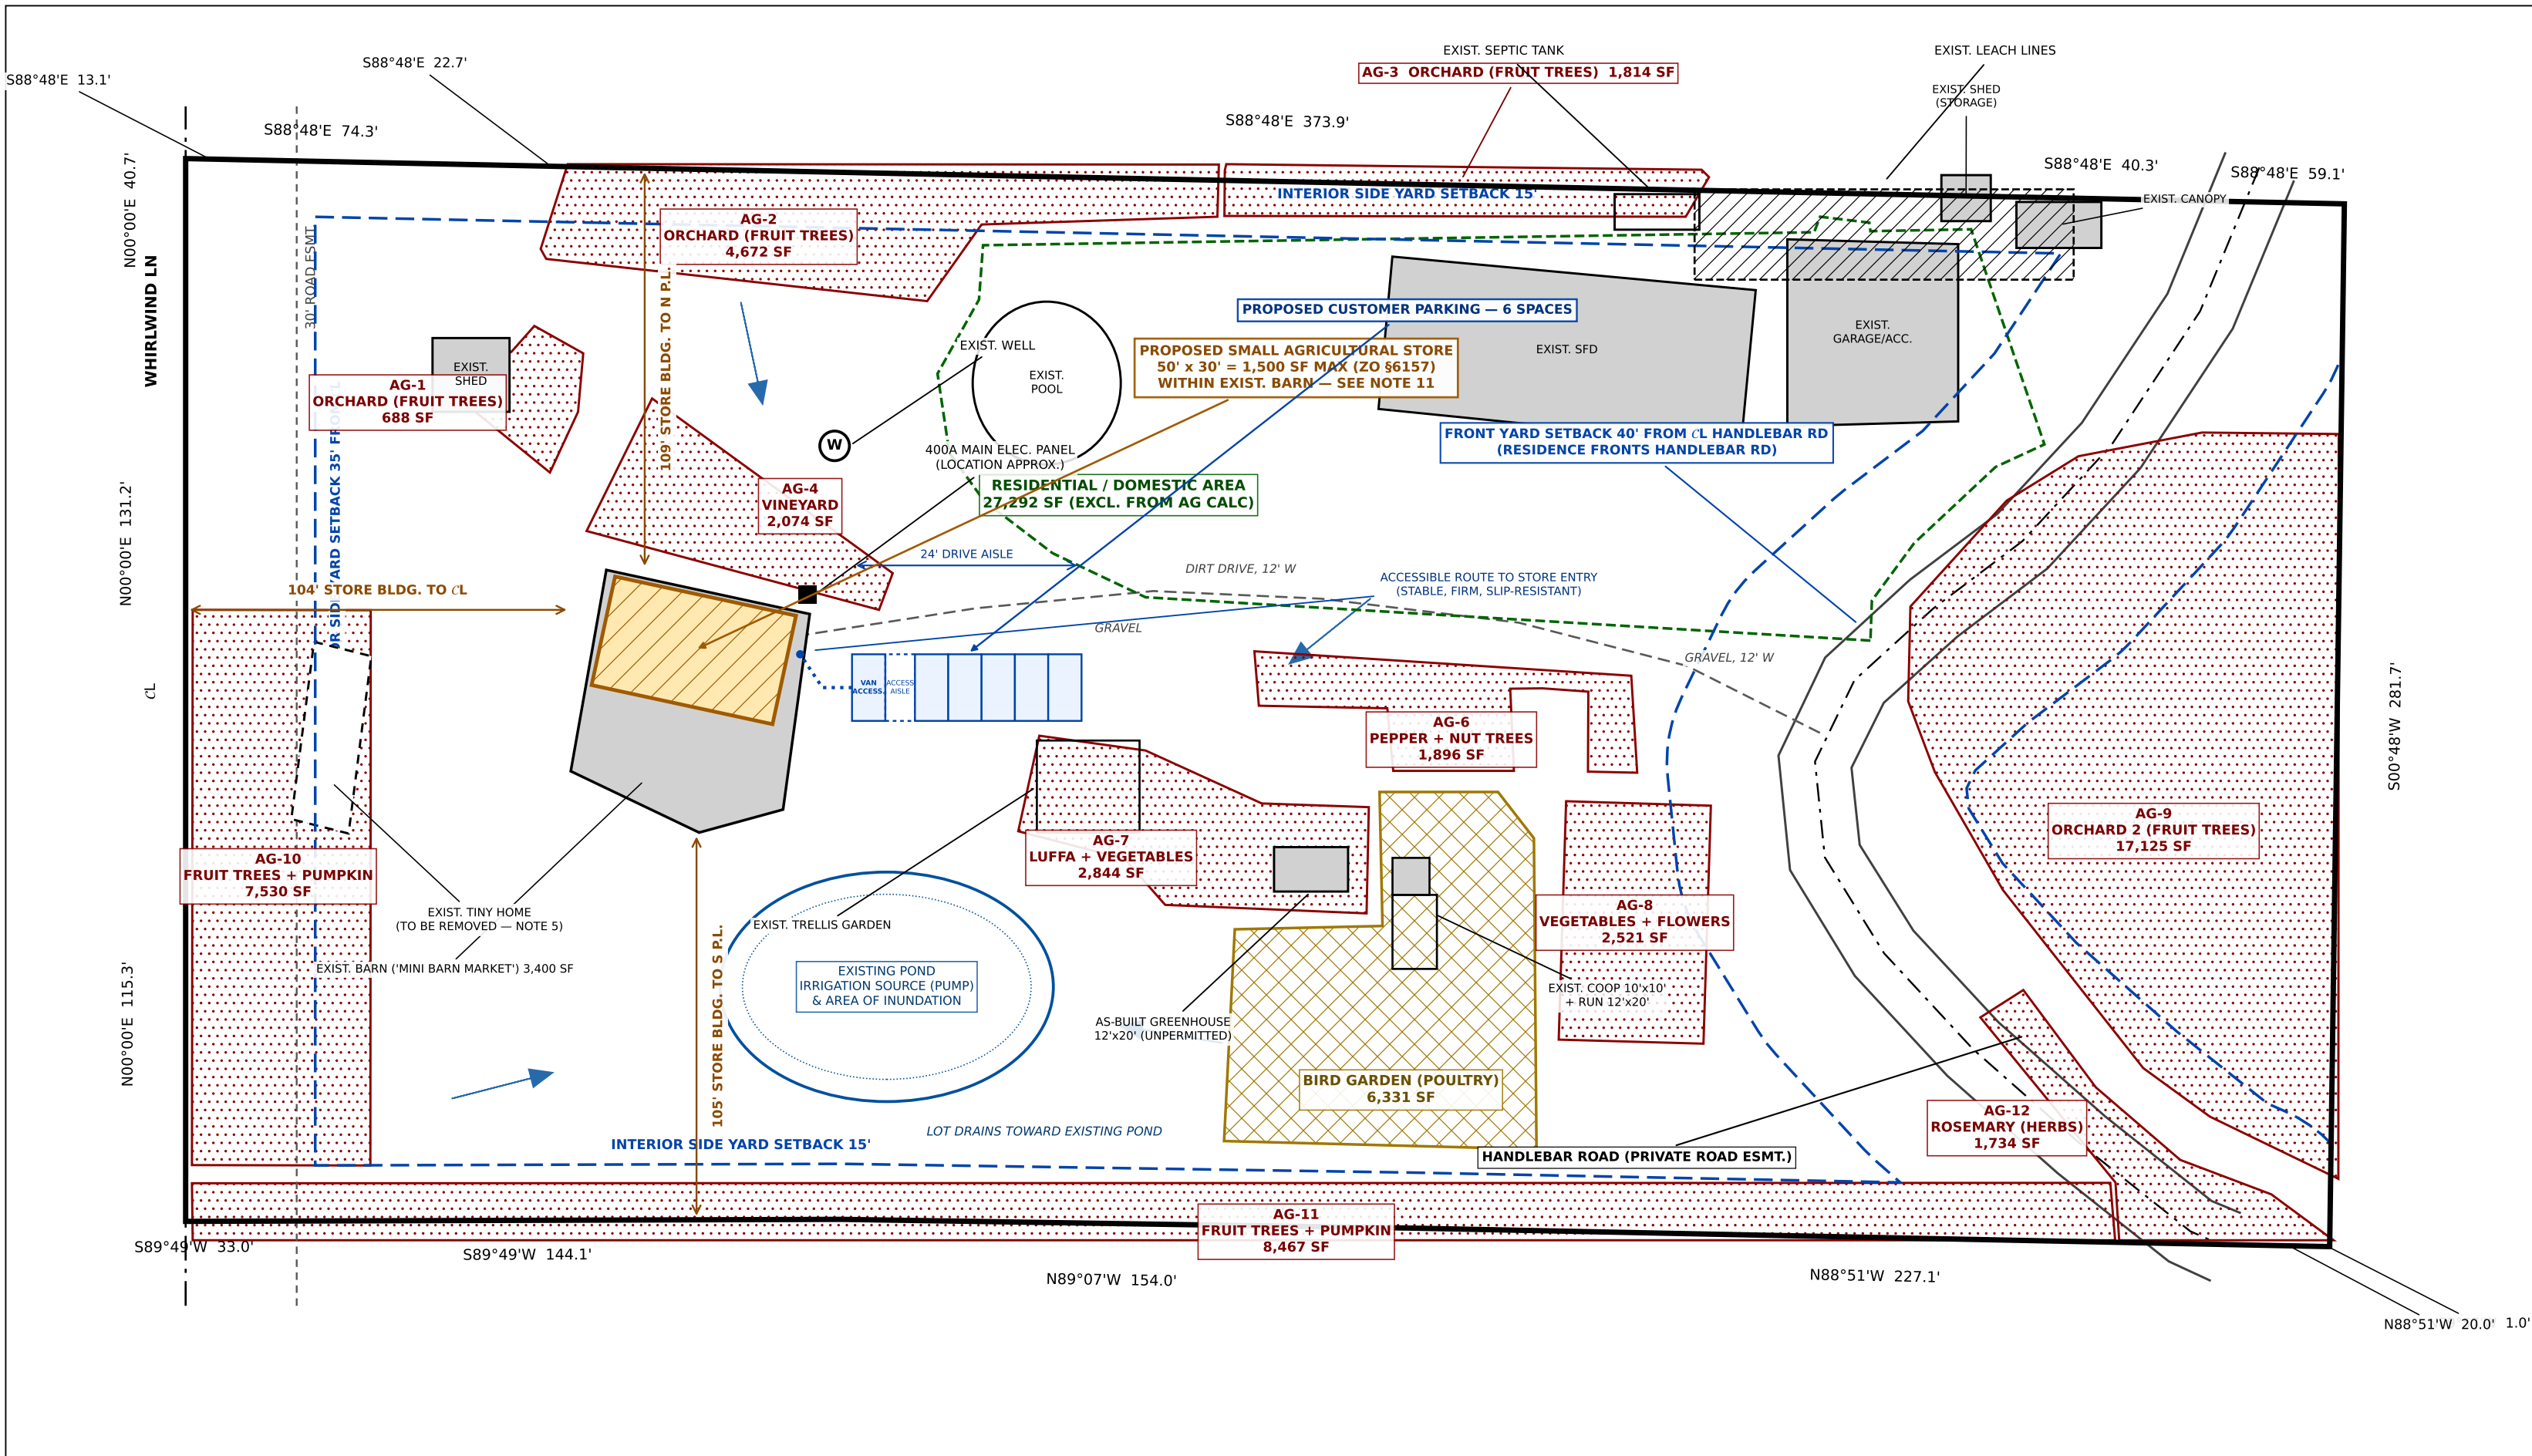

AGRICULTURAL OPERATIONS & SMALL AGRICULTURAL STORE PLOT PLAN

17054 HANDLEBAR ROAD, RAMONA, CA 92065

APN 278-361-08-00 · ZONE A70 (LIMITED AGRICULTURE)

ZONING BOX: A70 / L / 2AC / C / G / C / C

LEGAL: PARCEL 1 OF PARCEL MAP 05062 (FILE NO. 69370)

GROSS AREA: 164,443 SF (3.78 AC) · NET AREA: 157,251 SF (3.61 AC)

OWNER: CORY J. DZBINSKI & CARISSA ULTSCH

17054 HANDLEBAR RD, RAMONA, CA 92065

farmhousegetaways@gmail.com

PREPARED BY: OWNER

AGRICULTURAL USE SUMMARY

ZONE	USE / CROP	AREA
AG-1	ORCHARD (FRUIT TREES)	688 SF
AG-2	ORCHARD (FRUIT TREES)	4,672 SF
AG-3	ORCHARD (FRUIT TREES)	1,814 SF
AG-4	VINEYARD	2,074 SF
AG-6	PEPPER + NUT TREES	1,896 SF
AG-7	LUFFA + VEGETABLES	2,844 SF
AG-8	VEGETABLES + FLOWERS	2,521 SF
AG-9	ORCHARD 2 (FRUIT TREES)	17,125 SF
AG-10	FRUIT TREES + PUMPKIN	7,530 SF
AG-11	FRUIT TREES + PUMPKIN	8,467 SF
AG-12	ROSEMARY (HERBS)	1,734 SF
BG	BIRD GARDEN (POULTRY)	6,331 SF

TOTAL ACTIVE AGRICULTURAL AREA **57,696 SF**

= 35.1% OF GROSS (ZO §6157.a.2.b.ii REQ.: 25% = 41,111 SF)

AG-5 NOT USED — NUMBERING RETAINED PER OWNER FIELD NOTES. AREAS ARE AERIAL-DERIVED AND FIELD-CORROBORATED (NOTE 2).

STRUCTURE SUMMARY

STRUCTURE / USE	STATUS	FOOTPRINT
SMALL AGRICULTURAL STORE (IN BARN)	PROPOSED	1,500 SF
CUSTOMER PARKING, 6 SPACES	PROPOSED	1,116 SF
BARN ('MINI BARN MARKET')	EXISTING	3,400 SF
SFD — RESIDENCE (4BR/2BA, 2,724 SF LIV.)	EXISTING	4,110 SF
GARAGE / ACCESSORY BLDG	EXISTING	2,270 SF
SHED (NW) — STORAGE	EXISTING	415 SF
SHED (NE) — STORAGE	EXISTING	165 SF
CANOPY (NE)	EXISTING	285 SF
TRELLIS GARDEN (OPEN)	EXISTING	690 SF
GREENHOUSE 12'x20'	AS-BUILT	240 SF
POULTRY COOP 10'x10'	EXISTING	100 SF
POULTRY RUN 12'x20'	EXISTING	240 SF
POOL	EXISTING	1,380 SF
TINY HOME (W)	TO BE REMOVED	765 SF

NOTES

- BOUNDARY: SHOWN PER COUNTY GIS PARCEL POLYGON (164,443 SF). THE ASSESSOR'S MAP (BK 278 PG 36) SHOWS THE RECORD PARCEL AS 550.50' x 285.58' = 157,212 SF (3.61 AC). RECORDED PM 05062 GOVERNS AND IS NOT YET OBTAINED. THE AG-USE TESTS ARE MET ON EITHER BASIS.
- AG AREAS AND STRUCTURE FOOTPRINTS ARE AERIAL-DERIVED AND FIELD-CORROBORATED. THE SOURCE AERIAL IS CROPPED TO THE PARCEL, SO CROP AREAS RUN TO THE PROPERTY LINE. OWNER FIELD VERIFICATION CONTINUING. AG-9 LEGS MEASURED 200' (W ALONG RD), 130' (N), 190' (E FENCE); THE W AND N BOUNDARIES CURVE OUTWARD.
- NO GRADING AND NO NEW BUILDING PROPOSED. THIS PLAN DOCUMENTS EXISTING AG OPERATIONS AND A PROPOSED SMALL AGRICULTURAL STORE (ZO §6157).
- SETBACKS PER THE PARCEL ZONING BOX, DESIGNATOR C, ZO §4810 SCHEDULE C. THE RESIDENCE FRONTS HANDLEBAR RD, SO THAT IS THE FRONT YARD: 40' FROM ITS E PER SCHEDULE C. FOOTNOTE (d). A PRIVATE EASEMENT UNDER 40' WIDE. WHIRLWIND LN IS THE EXTERIOR SIDE YARD AT 35' FROM E; NORTH AND SOUTH ARE INTERIOR SIDE YARDS AT 15'. NO REAR YARD APPLIES — THE LOT FRONTS STREETS EAST AND WEST.
- EXISTING ACCESSORY STRUCTURES NEAR THE NORTH LINE (NE SHED 165 SF, NE CANOPY 285 SF) LIE PARTLY WITHIN THE INTERIOR SIDE YARD. PERMITTED UNDER ZO §4842: WALLS ≥3' FROM THE LOT LINE AND COMBINED AREA WITHIN THE SETBACK (450 SF) UNDER THE 1,000 SF LIMIT. THE TINY HOME LIES WITHIN THE 35' EXTERIOR SIDE YARD AND IS TO BE REMOVED. NO NEW WORK IS PROPOSED IN ANY YARD, AND THE PROPOSED STORE CLEARS EVERY REQUIRED YARD.
- POND IS AN EXISTING IRRIGATION SOURCE (PUMP) AND THE AREA OF INUNDATION; LOT DRAINS TO POND. WELL, SEPTIC AND LEACH LINES PER OWNER, APPROXIMATE.
- GREENHOUSE SHOWN AS-BUILT (UNPERMITTED); MAY QUALIFY FOR THE AGRICULTURAL BUILDING EXEMPTION — CONFIRM WITH PDS. ELECTRICAL: 400A MAIN PANEL NE OF BARN.
- DRIVEWAY RUNS E-W FROM HANDLEBAR RD; GRAVEL BOTH ENDS, DIRT MID-SEGMENT PAST THE RESIDENCE, 12' WIDE; SLOPE 2% DRAINING WEST TOWARD THE POND.
- WHIRLWIND LN & SHOWN AT THE WEST P.L. PER OWNER, WITH A 30' ROAD ESMT. ALONG THAT BOUNDARY. HANDLEBAR RD IS A PRIVATE ROAD ESMT. CROSSING THE EAST PORTION, & SHOWN: ASSESSOR'S MAP DIMENSIONS IT AS 30'. BOTH TO BE VERIFIED.
- NO NEW OR MODIFIED LANDSCAPE AREA PROPOSED (PDS 090 ITEM 16). EXISTING AG AND PERIMETER FENCING ONLY; HEIGHTS TO BE FIELD-VERIFIED AND ADDED PRIOR TO SUBMITTAL. NO NEW FENCES, WALLS OR GATES PROPOSED.
- ZO §6157.a.2.e LIMITS THE STORE TO 1,500 SF TOTAL INCLUDING OPEN ROOFED DISPLAY. IT IS SHOWN AS A DEMISED 1,500 SF PORTION OF THE EXISTING BARN; NO OTHER STRUCTURE WILL BE USED FOR ON-SITE SALES. PUBLIC AREAS TO BE PERMITTED AND BUILT TO THE COMMERCIAL BUILDING CODE AND DEHQ REQUIREMENTS. CONFIRM WITH PDS THAT A DEMISED PORTION OF A LARGER BUILDING SATISFIES §6157.a.2.e.
- ACCESSIBLE STALL, AISLE AND THE ROUTE TO THE STORE ENTRANCE TO BE A STABLE, FIRM, SLIP-RESISTANT SURFACE PER CBC CH. 11B AND §6157.a.2.h.

AGRICULTURAL OPERATIONS & SMALL AGRICULTURAL STORE

PLOT PLAN — EXISTING CONDITIONS & PROPOSED STORE

17054 HANDLEBAR RD, RAMONA, CA 92065

APN 278-361-08-00 · ZONE A70

SCALE: 1" = 40'

DATE: 8/19/2026

SHEET 1 OF 1

REV DATE DESCRIPTION

- | | | |
|---|-----------|-------------------------------------|
| 4 | 8/06/2026 | BASE SHEET |
| 5 | 8/06/2026 | SETBACK LINES ADDED |
| 6 | 8/19/2026 | FARM STORE ADDED |
| 7 | 8/19/2026 | SETBACKS & AREAS PER TRUE LOT LINES |

AGRICULTURAL USE CALCULATION

PER ZO §6157.a.2.b — GROSS BASIS

TOTAL GROSS AREA OF PREMISES 164,443 SF

b.i REQUIRED 50% SUITABLE / AVAILABLE 82,222 SF

PROVIDED (GROSS LESS RESIDENTIAL) 137,151 SF

= 83.4% OF GROSS PASSES

b.ii REQUIRED 25% IN ACTIVE AG USE 41,111 SF

CROP AREAS AG-1 THRU AG-12 51,365 SF

POULTRY (BIRD GARDEN) 6,331 SF

PROVIDED TOTAL ACTIVE AG USE 57,696 SF

= 35.1% OF GROSS PASSES

MARGIN OVER THE 25% REQUIREMENT +16,585 SF

BOTH ZO §6157.a.2.b THRESHOLDS ARE MET

ON THE RECORD PARCEL (157,212 SF — SEE BOUNDARY NOTE)

AG USE IS 36.7% — THE TESTS ARE MET ON EITHER BASIS.

NET AREA EXCL. ROAD ESMTS. (PDS 090 ITEM 12): 157,251 SF

SMALL AGRICULTURAL STORE

COMPLIANCE — ZONING ORDINANCE §6157.a.2

(ZO UPDATE 102, PUBLISHED 3-26-2020)

§6157C COMMERCIAL AG MUST BE THE PRINCIPAL USE SEE b.i / b.ii

a PERMITTED IN A70 USE REGS. A70 — NO MIN. LOT SIZE

b.i ≥50% OF GROSS SUITABLE/AVAILABLE 83.4% PROVIDED

b.ii ≥25% OF GROSS IN ACTIVE AG USE 35.1% PROVIDED

c OPERATED BY OWNER OR TENANT OWNER-OPERATED

d ONE STORE PER LEGAL LOT; NO EXIST. NONE EXISTING

e AG STAND OR LARGE AG STORE 1,500 SF SHOWN

STORE ≤1,500 SF INCL. ROOFED DISPLAY 3,500 SF SHOWN

CONFORM TO §4810 SETBACKS STORE CLEARS ALL YARDS

PUBLIC AREAS TO COMM. BLDG. CODE + DEHQ SEE NOTE 11

f RETAIL ONLY WITH ON-SITE PRODUCE / EGGS; ACKNOWLEDGED

g AG WEIGHTS & MEASURES REGS. APPLY TO BE DESIGNATED

h ≤200 SF FOR OFF-SITE PRODUCTS 6 SHOWN, GRAVEL

i MINIMUM 6 PARKING SPACES 1 VAN ACCESSIBLE

j DISABLED ACCESS PER CBC CH. 11B ACKNOWLEDGED

k HOURS 10 A.M. TO LEGAL SUNSET ACKNOWLEDGED

l ONE ON-PREMISE SIGN, MAX 4 SF ACKNOWLEDGED

m EVENTS PROHIBITED ACKNOWLEDGED

STORE AREA SUMMARY

PROPOSED STORE FLOOR AREA 1,500 SF

OF WHICH OFF-SITE PRODUCTS (MAX) 200 SF

OPEN ROOFED DISPLAY AREA 0 SF

TOTAL PER §6157.a.2.e — LIMIT 1,500 SF 1,500 SF

PARKING — ZO §6157.a.2.h

REQUIRED 6 SPACES

PROVIDED 6 SPACES

STANDARD 9' x 18' 5

VAN ACCESSIBLE 9' x 18' + 8' AISLE 1

SURFACE — GRAVEL (EXPRESSLY ALLOWED) PROPOSED

OUTSTANDING — CONFIRM WITH PDS ZONING

§6157.a.2.e LIMITS THE STORE TO 1,500 SF. THE EXISTING BARN IS LARGER. CONFIRM A DEMISED ≤1,500 SF PORTION SATISFIES IT, OR SITE THE STORE IN A SEPARATE ≤1,500 SF STRUCTURE.

LEGEND

- PROPOSED SMALL AGRICULTURAL STORE
- PROPOSED CUSTOMER PARKING
- AGRICULTURAL CROP AREA
- POULTRY AREA (BIRD GARDEN)
- RESIDENTIAL / DOMESTIC AREA
- EXISTING STRUCTURE
- STRUCTURE TO BE REMOVED
- LEACH LINES
- ROAD CENTERLINE
- ROAD EASEMENT LINE
- REQUIRED YARD SETBACK
- DRIVEWAY CENTERLINE
- DIRECTION OF LOT DRAINAGE
- EXISTING WELL

STORMWATER (PDS 272)

PROPOSED LAND DISTURBANCE: 0 SF. NO GRADING, CLEARING OR

CONSTRUCTION PROPOSED; NO NEW OR REPLACED IMPERVIOUS AREA.

SD-B: RUNOFF DIRECTED TO PERVIOUS/LANDSCAPED AREAS.

SD-G: EXISTING NATURAL SWALES AND POND CONSERVED.

SD-H: VEGETATED BUFFER MAINTAINED AROUND EXISTING POND.

VICINITY MAP

(NOT TO SCALE)

