

AGRICULTURAL OPERATIONS & SMALL AGRICULTURAL STORE PLOT PLAN

17054 HANDLEBAR ROAD, RAMONA, CA 92065

APN 278-361-08-00 · ZONE A70 (LIMITED AGRICULTURE)

ZONING BOX: A70 / L / 2AC / C / G / C / C

LEGAL: PARCEL 1 OF PARCEL MAP 05062 (FILE NO. 69370)

GROSS AREA: 164,443 SF (3.78 AC) · NET AREA: 157,251 SF (3.61 AC)

OWNER: CORY J. DZBINSKI & CARISSA ULTSCH

17054 HANDLEBAR RD, RAMONA, CA 92065

farmhousegetaways@gmail.com

PREPARED BY: OWNER

AGRICULTURAL USE SUMMARY

ZONE	USE / CROP	AREA
AG-1	ORCHARD (FRUIT TREES)	688 SF
AG-2	ORCHARD (FRUIT TREES)	4,672 SF
AG-3	ORCHARD (FRUIT TREES)	1,814 SF
AG-4	VINEYARD	2,074 SF
AG-6	PEPPER + NUT TREES	1,896 SF
AG-7	LUFFA + VEGETABLES	2,844 SF
AG-8	VEGETABLES + FLOWERS	2,521 SF
AG-9	ORCHARD 2 (FRUIT TREES)	17,125 SF
AG-10	FRUIT TREES + PUMPKIN	7,530 SF
AG-11	FRUIT TREES + PUMPKIN	8,467 SF
AG-12	ROSEMARY (HERBS)	1,734 SF
BG	BIRD GARDEN (POULTRY)	6,331 SF

TOTAL ACTIVE AGRICULTURAL AREA 57,696 SF

= 35.1% OF GROSS (ZO §6157 REQ.: 25% = 41,111 SF)

AG-5 NOT USED — NUMBERING RETAINED PER OWNER FIELD NOTES.

STRUCTURE SUMMARY

STRUCTURE / USE	STATUS	FOOTPRINT
SMALL AGRICULTURAL STORE (IN BARN)	PROPOSED	1,500 SF
CUSTOMER PARKING, 6 SPACES	PROPOSED	1,116 SF
BARN ('MINI BARN MARKET')	EXISTING	3,400 SF
SFD — RESIDENCE (4BR/2BA, 2,724 SF LIV.)	EXISTING	4,110 SF
GARAGE / ACCESSORY BLDG	EXISTING	2,270 SF
SHED (NW) — STORAGE	EXISTING	415 SF
SHED (NE) — STORAGE	EXISTING	165 SF
CANOPY (NE)	EXISTING	285 SF
TRELLIS GARDEN (OPEN)	EXISTING	690 SF
GREENHOUSE 12'x20'	AS-BUILT	240 SF
POULTRY COOP 10'x10'	EXISTING	100 SF
POULTRY RUN 12'x20'	EXISTING	240 SF
POOL	EXISTING	1,380 SF
TINY HOME (W)	TO BE REMOVED	765 SF

FOOTPRINTS AERIAL-DERIVED, APPROXIMATE (NOTE 2).

NOTES

- PARCEL BOUNDARY PER COUNTY GIS / PM 05062; BEARINGS AND DISTANCES GIS-DERIVED (APPROXIMATE). RECORD BEARINGS PER PM 05062. ALL DIMENSIONS IN FEET.
- AG AREAS AND STRUCTURE FOOTPRINTS AERIAL-MEASURED AND FIELD-CORROBORATED; OWNER FIELD VERIFICATION CONTINUING.
- NO NEW CONSTRUCTION OR GRADING PROPOSED. PLAN DOCUMENTS EXISTING AG OPERATIONS AND A PROPOSED SMALL AGRICULTURAL STORE PER ZO §6157.
- SETBACKS PER ZONING BOX SETBACK DESIGNATOR C, ZO §4810 SCHEDULE C: FRONT 60' FROM CL; INTERIOR SIDE 15' FROM LOT LINE; EXTERIOR SIDE 35' FROM CL; REAR 25' FROM LOT LINE. FOOTNOTE (d): A LOT FRONTING A PRIVATE EASEMENT UNDER 40' WIDE TAKES A 40' FRONT YARD FROM CL. FRONTAGE DETERMINATION TO BE CONFIRMED WITH PDS ZONING (858) 694-8985 — ALL STRUCTURES CLEAR EVERY YARD EITHER WAY.
- EXIST. NE SHED (165 SF) AND CANOPY (285 SF) LIE WITHIN THE INTERIOR SIDE YARD. PERMITTED UNDER ZO §4842; WALLS ≥3' FROM THE LOT LINE. COMBINED AREA WITHIN THE SETBACK (450 SF) UNDER THE 1,000 SF LIMIT.
- POND IS AN EXISTING IRRIGATION SOURCE (PUMP) AND THE AREA OF INUNDATION; LOT DRAINS TO POND, WELL, SEPTIC AND LEACH LINES PER OWNER, APPROXIMATE.
- GREENHOUSE SHOWN AS-BUILT (UNPERMITTED); MAY QUALIFY FOR THE AGRICULTURAL BUILDING EXEMPTION — CONFIRM WITH PDS.
- DRIVEWAY RUNS EW FROM HANDLEBAR RD; GRAVEL BOTH ENDS, DIRT MID-SEGMENT PAST THE RESIDENCE; SLOPE ≈5%, DRAINING WEST TOWARD THE POND.
- ELECTRICAL-400A MAIN PANEL ADJACENT NE OF BARN.
- WHIRLWIND LN & SHOWN COINCIDENT WITH THE WEST PROPERTY LINE AND THE 30' ROAD ESMT. WIDTH ASSUMED — BOTH TO BE VERIFIED AGAINST RECORDED PM 05062.
- EXIST. TINY HOME SITS 29' FROM THE WEST PROPERTY LINE, WITHIN THE 35' EXTERIOR SIDE YARD. REMOVAL (PLANNED) RESOLVES THE ENCRoACHMENT.
- HANDLEBAR RD IS A PRIVATE ROAD ESMT. CROSSING THE EAST PORTION; § SHOWN. WIDTH PER PM 05062 TO BE VERIFIED — ASSESSOR'S MAP SHOWS 30' WHERE DIMENSIONED.
- NO NEW OR MODIFIED LANDSCAPE AREA PROPOSED (PDS 090 ITEM 16). EXISTING AG AND PERIMETER FENCING ONLY; HEIGHTS TO BE FIELD-VERIFIED, NO NEW FENCES, WALLS OR GATES PROPOSED (PDS 070; FENCES ≤6' EXEMPT FROM BUILDING PERMIT).
- ZO §6157(e) LIMITS THE STORE TO 1,500 SF TOTAL INCLUDING OPEN ROOFED DISPLAY. THE STORE IS SHOWN AS A DEMISED 1,500 SF PORTION OF THE EXIST. BARN; NO OTHER STRUCTURE WILL BE USED FOR ON-SITE SALES. PUBLIC-ACCESSED AREAS TO BE PERMITTED AND BUILT TO THE APPLICABLE COMMERCIAL BUILDING CODE AND DEHO REQUIREMENTS. CONFIRM WITH PDS THAT A DEMISED PORTION OF A LARGER BUILDING SATISFIES §6157(e).

AGRICULTURAL OPERATIONS & SMALL AGRICULTURAL STORE

PLOT PLAN — EXISTING CONDITIONS & PROPOSED STORE

17054 HANDLEBAR RD, RAMONA, CA 92065

APN 278-361-08-00 · ZONE A70

SCALE: 1" = 40'

DATE: 8/19/2026


SHEET 1 OF 1

REV DATE DESCRIPTION

4 8/06/2026 BASE SHEET

5 8/06/2026 SETBACK LINES ADDED

6 8/19/2026 FARM STORE; SETBACKS CORRECTED PER §4810

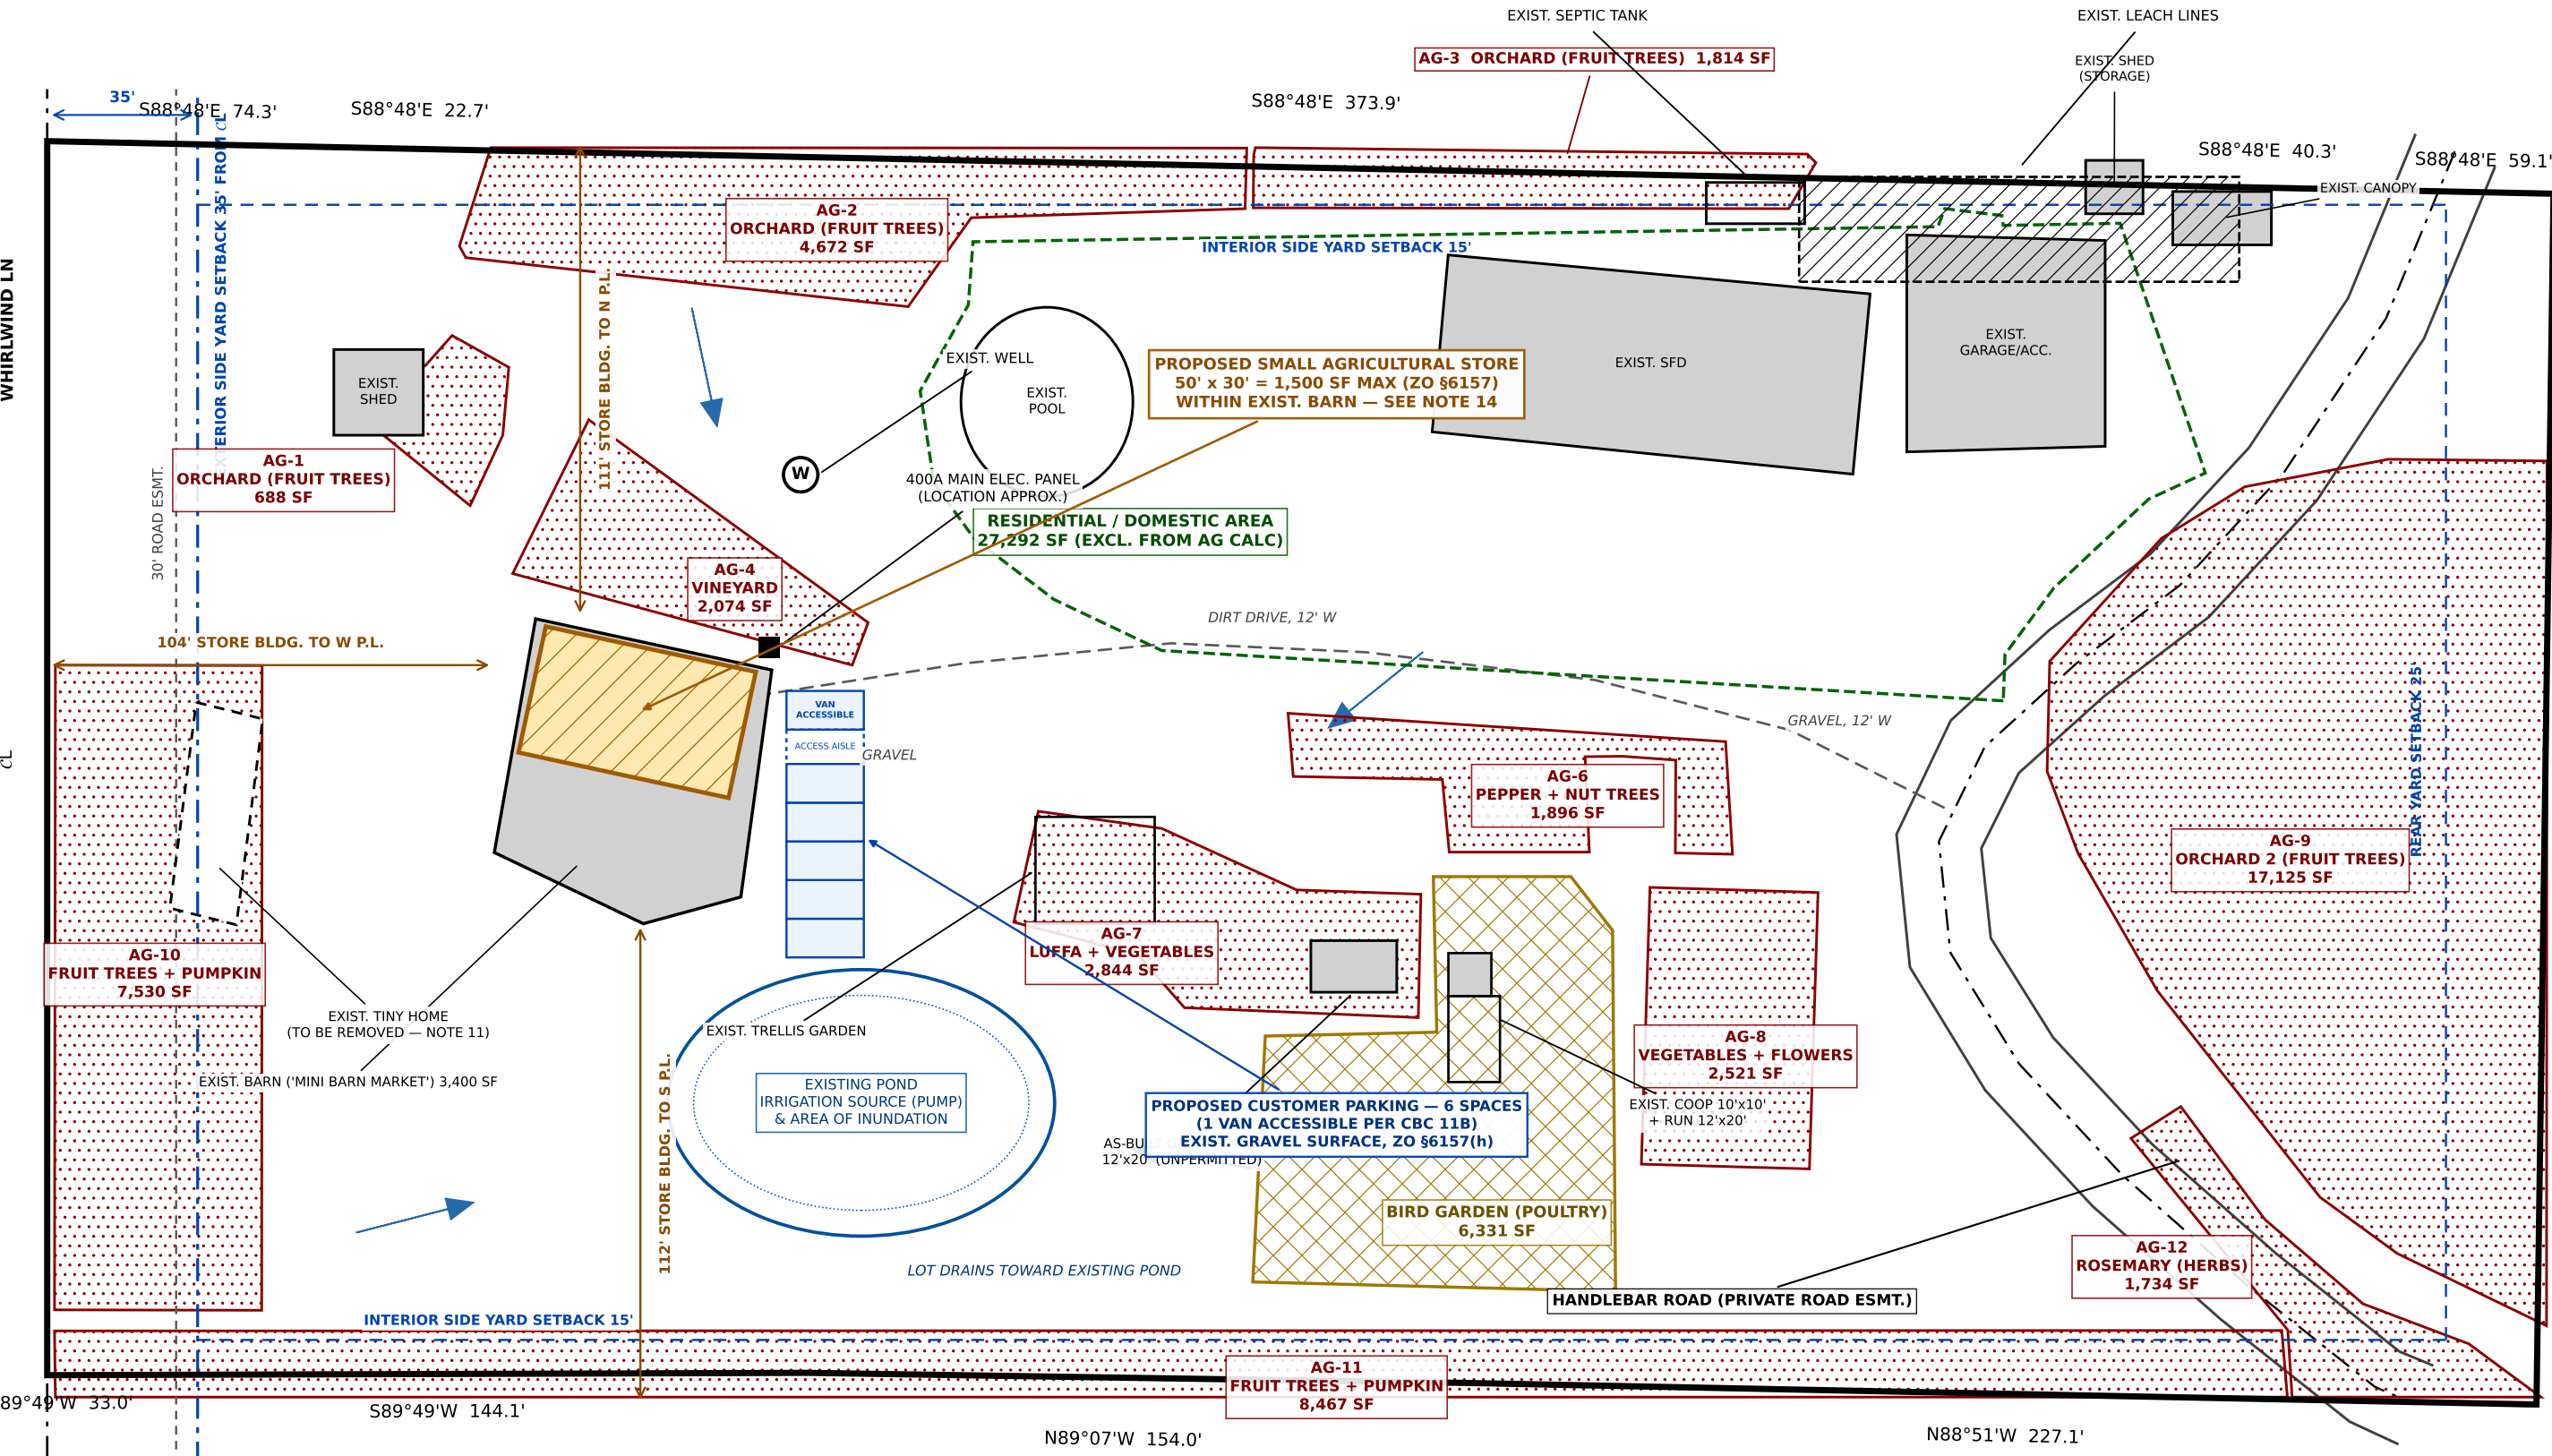

AGRICULTURAL USE CALCULATION

PER ZO §6157(b) — GROSS BASIS

TOTAL GROSS AREA OF PREMISES 164,443 SF
(COUNTY GIS PARCEL POLYGON, 3.78 AC)

REQUIRED — 50% SUITABLE & AVAILABLE 82,222 SF

PROVIDED — GROSS LESS RESIDENTIAL 137,151 SF
= 83.4% OF GROSS PASSES

REQUIRED — 25% ACTIVE AG USE 41,111 SF

CROP AREAS AG-1 THRU AG-12 51,365 SF

POULTRY (BIRD GARDEN) 6,331 SF

PROVIDED — TOTAL ACTIVE AG USE 57,696 SF
= 35.1% OF GROSS PASSES


MARGIN OVER 25% REQUIREMENT +16,585 SF

BOTH ZO §6157(b) THRESHOLDS ARE MET

NET AREA EXCL. ROAD ESMTS. (PDS 090 ITEM 12): 157,251 SF
ON THE NET BASIS AG USE IS 36.7% — MET EITHER WAY.

N

GRAPHIC SCALE: 1" = 40'

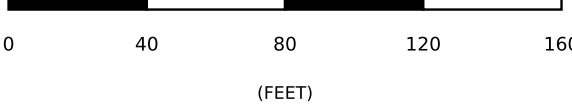

SMALL AGRICULTURAL STORE

COMPLIANCE — ZONING ORDINANCE §6157
(ZO UPDATE 102, ADOPTED 3-26-2020)

a	PERMITTED IN A70 USE REGS.	A70 — NO MIN. LOT SIZE
	NO ZONING VERIFICATION PERMIT REQ'D	PERMITTED BY RIGHT
b.i	≥50% OF GROSS SUITABLE/AVAILABLE	83.4% PROVIDED
b.ii	≥25% OF GROSS IN ACTIVE AG USE	35.1% PROVIDED
c	OPERATED BY OWNER OR TENANT	OWNER-OPERATED
d	ONE STORE PER LEGAL LOT; NO EXIST. AG STAND OR LARGE AG STORE	NONE EXISTING
e	STORE ≤1,500 SF INCL. ROOFED DISPLAY CONFORM TO §4810 SETBACKS	1,500 SF SHOWN CLEARS BY 104'/111'/112'
	PUBLIC AREAS TO COMM. BLDG. CODE + DEH	SEE NOTE 14
g	≤200 SF FOR OFF-SITE PRODUCTS	TO BE DESIGNATED
h	MINIMUM 6 PARKING SPACES DISABLED ACCESS PER CBC CH. 11B	6 SHOWN, GRAVEL 1 VAN ACCESSIBLE
i	HOURS 10 A.M. TO LEGAL SUNSET	ACKNOWLEDGED
j	ONE ON-PREMISE SIGN, MAX 4 SF	ACKNOWLEDGED
k	EVENTS PROHIBITED	ACKNOWLEDGED

STORE AREA SUMMARY

PROPOSED STORE FLOOR AREA	1,500 SF
OF WHICH OFF-SITE PRODUCTS (MAX)	200 SF
OPEN ROOFED DISPLAY AREA	0 SF
TOTAL PER §6157(e) — LIMIT 1,500 SF	1,500 SF

PARKING — ZO §6157(h)

REQUIRED	6 SPACES
PROVIDED	6 SPACES
STANDARD 9' x 18'	5
VAN ACCESSIBLE 9' x 18' + 8' AISLE	1
SURFACE — GRAVEL (EXPRESSLY ALLOWED)	EXISTING

OUTSTANDING — CONFIRM WITH PDS ZONING

§6157(e) LIMITS THE STORE TO 1,500 SF. THE EXIST. BARN IS LARGER. CONFIRM A DEMISED ≤1,500 SF PORTION SATISFIES §6157(e), OR SITE THE STORE IN A SEPARATE ≤1,500 SF STRUCTURE.

LEGEND

	PROPOSED SMALL AGRICULTURAL STORE
	PROPOSED CUSTOMER PARKING
	AGRICULTURAL CROP AREA
	POULTRY AREA (BIRD GARDEN)
	RESIDENTIAL / DOMESTIC AREA
	EXISTING STRUCTURE
	STRUCTURE TO BE REMOVED
	LEACH LINES
	ROAD CENTERLINE
	ROAD EASEMENT LINE
	REQUIRED YARD SETBACK
	DRIVEWAY CENTERLINE
	DIRECTION OF LOT DRAINAGE
	EXISTING WELL


STORMWATER (PDS 272)

PROPOSED LAND DISTURBANCE: 0 SF. NO GRADING, CLEARING OR CONSTRUCTION PROPOSED; NO NEW OR REPLACED IMPERVIOUS AREA.
SD-B: RUNOFF DIRECTED TO PERVIOUS/LANDSCAPED AREAS.
SD-G: EXISTING NATURAL SWALES AND POND CONSERVED.
SD-H: VEGETATED BUFFER MAINTAINED AROUND EXISTING POND.

VICINITY MAP

(NOT TO SCALE)

HIGHLAND VALLEY RD

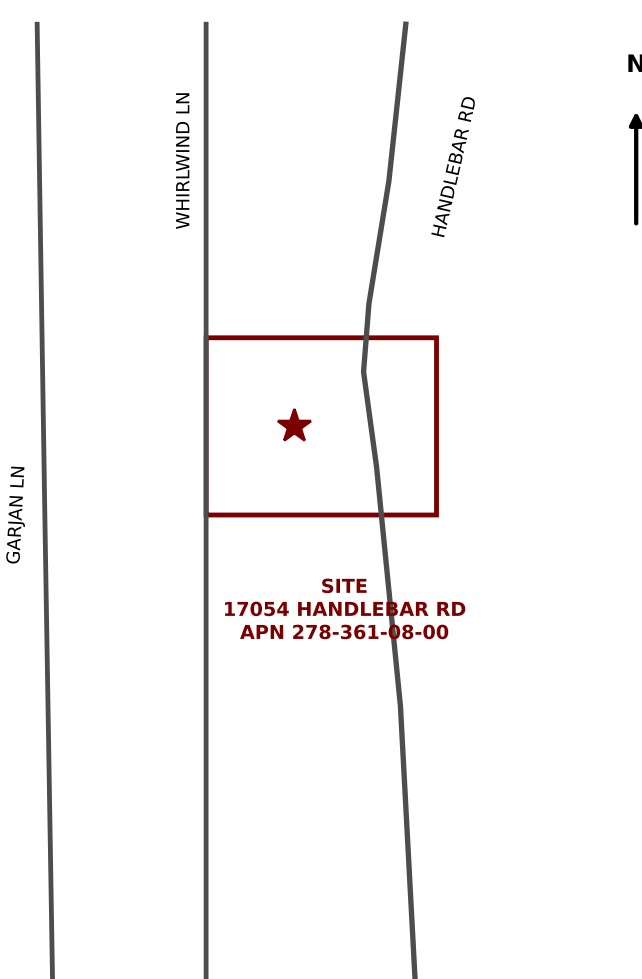

RAMONA, SAN DIEGO COUNTY, CALIFORNIA