

AGRICULTURAL OPERATIONS & SMALL AGRICULTURAL STORE PLOT PLAN

17054 HANDLEBAR ROAD, RAMONA, CA 92065

APN 278-361-08-00 · ZONE A70 (LIMITED AGRICULTURE)

ZONING BOX: A70 / L / 2AC / C / G / C / C

LEGAL: PARCEL 1 OF PARCEL MAP 05062 (FILE NO. 69370)

GROSS AREA: 164,443 SF (3.78 AC) · NET AREA: 157,251 SF (3.61 AC)

OWNER: CORY J. DZBINSKI & CARISSA ULTSCH

17054 HANDLEBAR RD, RAMONA, CA 92065

farmhousegetaways@gmail.com

PREPARED BY: OWNER

AGRICULTURAL USE SUMMARY

ZONE	USE / CROP	AREA
AG-1	ORCHARD (FRUIT TREES)	688 SF
AG-2	ORCHARD (FRUIT TREES)	4,672 SF
AG-3	ORCHARD (FRUIT TREES)	1,814 SF
AG-4	VINEYARD	2,074 SF
AG-6	PEPPER + NUT TREES	1,896 SF
AG-7	LUFFA + VEGETABLES	2,844 SF
AG-8	VEGETABLES + FLOWERS	2,521 SF
AG-9	ORCHARD 2 (FRUIT TREES)	17,125 SF
AG-10	FRUIT TREES + PUMPKIN	7,530 SF
AG-11	FRUIT TREES + PUMPKIN	8,467 SF
AG-12	ROSEMARY (HERBS)	1,734 SF
BG	BIRD GARDEN (POULTRY)	6,331 SF

TOTAL ACTIVE AGRICULTURAL AREA 57,696 SF

= 35.1% OF GROSS (ZO §6157.a.2.b.ii REQ.: 25% = 41,111 SF)

AG-5 NOT USED — NUMBERING RETAINED PER OWNER FIELD NOTES. AREAS ARE AERIAL-DERIVED AND FIELD-CORROBORATED (NOTE 2).

STRUCTURE SUMMARY

STRUCTURE / USE	STATUS	FOOTPRINT
MINI BARN MARKET — SMALL AG. STORE 12'x10'	PROPOSED	120 SF
STORAGE BLDG 10'x10' (ADJ. TO STORE — NO SALES)	EXISTING	100 SF
CUSTOMER PARKING, 6 SPACES	PROPOSED	1,116 SF
BARN — STORAGE 50'x44'	EXISTING	2,200 SF
SFD — RESIDENCE (4BR/2BA, 2,724 SF LIV.)	EXISTING	4,110 SF
GARAGE / ACCESSORY BLDG	EXISTING	2,270 SF
TRELLIS GARDEN (OPEN)	EXISTING	690 SF
GREENHOUSE 12'x20'	AS-BUILT	240 SF
POULTRY COOP 10'x10'	EXISTING	100 SF
POULTRY RUN 12'x20'	EXISTING	240 SF
POOL	EXISTING	1,380 SF
TINY HOME (W)	TO BE REMOVED	765 SF

FOOTPRINTS AERIAL-DERIVED, APPROXIMATE (NOTE 2).

NOTES

- PARCEL BOUNDARY PER COUNTY GIS / PM 05062, OWNER-VERIFIED AGAINST THE SITE AERIAL. BEARINGS AND DISTANCES ARE GIS-DERIVED (APPROXIMATE); RECORD BEARINGS AND DIMENSIONS PER RECORDED PM 05062. ALL DIMENSIONS IN FEET.
- AG AREAS AND STRUCTURE FOOTPRINTS AERIAL-DERIVED, FIELD-CORROBORATED, AND PER OWNER MEASUREMENT WHERE STATED (STORE 12'x10', STORAGE 10'x10', BARN 50'x44'). CROP AREAS ARE DRAWN CLIPPED TO THE PARCEL BOUNDARY; TABULATED AREAS PER OWNER. AG-3 STOPS AT THE FENCE ~20' W OF THE SEPTIC TANK. AG-9 LEGS MEASURED 200' (W), 130' (N), 190' (E FENCE); W AND N SIDES CURVE OUT.
- NO GRADING PROPOSED. THE ONLY NEW CONSTRUCTION IS THE 12'x10' STORE (UNDER CONSTR.). PLAN DOCUMENTS EXISTING AG OPERATIONS + PROPOSED STORE (ZO §6157).
- SETBACKS PER THE PARCEL ZONING BOX, DESIGNATOR C, ZO §4810 SCHEDULE C, ALL MEASURED FROM THE PROPERTY LINES: NORTH AND SOUTH INTERIOR SIDE YARDS 15', EAST REAR YARD 25', WEST EXTERIOR SIDE YARD 35' FROM WHIRLWIND LN & (SHOWN AT THE WEST P.L. PER OWNER — NOTE 9). YARD DESIGNATIONS TO BE CONFIRMED WITH PDS AT SUBMITTAL.
- THE PROPOSED STORE SITS IN THE BUILDABLE AREA, CLEAR OF EVERY REQUIRED YARD (22' BEYOND THE WHIRLWIND SETBACK, 60' + ELSEWHERE). EXIST. TINY HOME (W) IS TO BE REMOVED. ROAD CENTRELINES ARE APPROXIMATE PENDING PM 05062 (NOTE 9).
- POND IS RUNOFF-FED (NO PUMP); IRRIGATION SOURCE & AREA OF INUNDATION; LOT DRAINS TO POND, WELL, SEPTIC AND LEACH LINES PER OWNER, APPROXIMATE.
- GREENHOUSE SHOWN AS-BUILT, MAY QUALIFY FOR THE AGRICULTURAL BUILDING EXEMPTION — CONFIRM WITH PDS. ELECTRICAL: 400A MAIN PANEL NE OF BARN.
- DRIVEWAY RUNS FROM THE STORE/PARKING YARD (NW) S PAST AG-1 AND THE BARN, E PAST THE RESIDENCE, THEN SE BETWEEN AG-9 AND AG-12, LEAVING THE PARCEL NEAR THE SE CORNER AND CONTINUING ±700' TO HANDLEBAR RD VIA AN ACCESS ESMT. ACROSS THE ADJACENT PARCEL. GRAVEL BOTH ENDS, DIRT MID-SEGMENT.
- WHIRLWIND LN & SHOWN AT THE WEST P.L. PER OWNER, WITH A 30' ROAD ESMT. ALONG THAT BOUNDARY. HANDLEBAR RD DOES NOT TOUCH THE PARCEL — ACCESS IS BY THE DRIVEWAY AND ESMT. OF NOTE 8. ESMT. GEOMETRY PER RECORDED PM 05062, TBD.
- NO NEW OR MODIFIED LANDSCAPE AREA PROPOSED (PDS 090 ITEM 16). EXISTING AG AND PERIMETER FENCING ONLY; HEIGHTS TO BE FIELD-VERIFIED AND ADDED PRIOR TO SUBMITTAL. NO NEW FENCES, WALLS OR GATES PROPOSED.
- THE PROPOSED SMALL AGRICULTURAL STORE IS THE NEW 'MINI BARN MARKET', A 12'x10' = 120 SF BUILDING UNDER CONSTRUCTION — WELL UNDER THE 1,500 SF LIMIT OF §6157.a.2.e INCL. OPEN ROOFED DISPLAY (NONE). THE ADJACENT 10'x10' BLDG IS STORAGE ONLY; NO OTHER STRUCTURE WILL BE USED FOR ON-SITE SALES. PUBLIC-ACCESSED AREAS TO BE PERMITTED TO COMM. BLDG. CODE AND DEHQ REQUIREMENTS.
- ACCESSIBLE STALL, AISLE AND THE ROUTE TO THE STORE ENTRANCE TO BE A STABLE, FIRM, SLIP-RESISTANT SURFACE PER CBC CH. 11B AND §6157.a.2.h.

AGRICULTURAL OPERATIONS & SMALL AGRICULTURAL STORE

PLOT PLAN — EXISTING CONDITIONS & PROPOSED STORE

17054 HANDLEBAR RD, RAMONA, CA 92065

APN 278-361-08-00 · ZONE A70

SCALE: 1" = 40'

DATE: 8/22/2026

SHEET 1 OF 1 · REV 19


REV DATE DESCRIPTION

4-6 8/06-8/19 BASE, SETBACKS, FARM STORE

7-16 8/21/2026 OWNER CORRECTION ROUNDS

17-18 8/22/2026 NO ROAD; STORE PER MARKUP

19 8/22/2026 DRIVEWAY RE-TRACED PER MARKUP

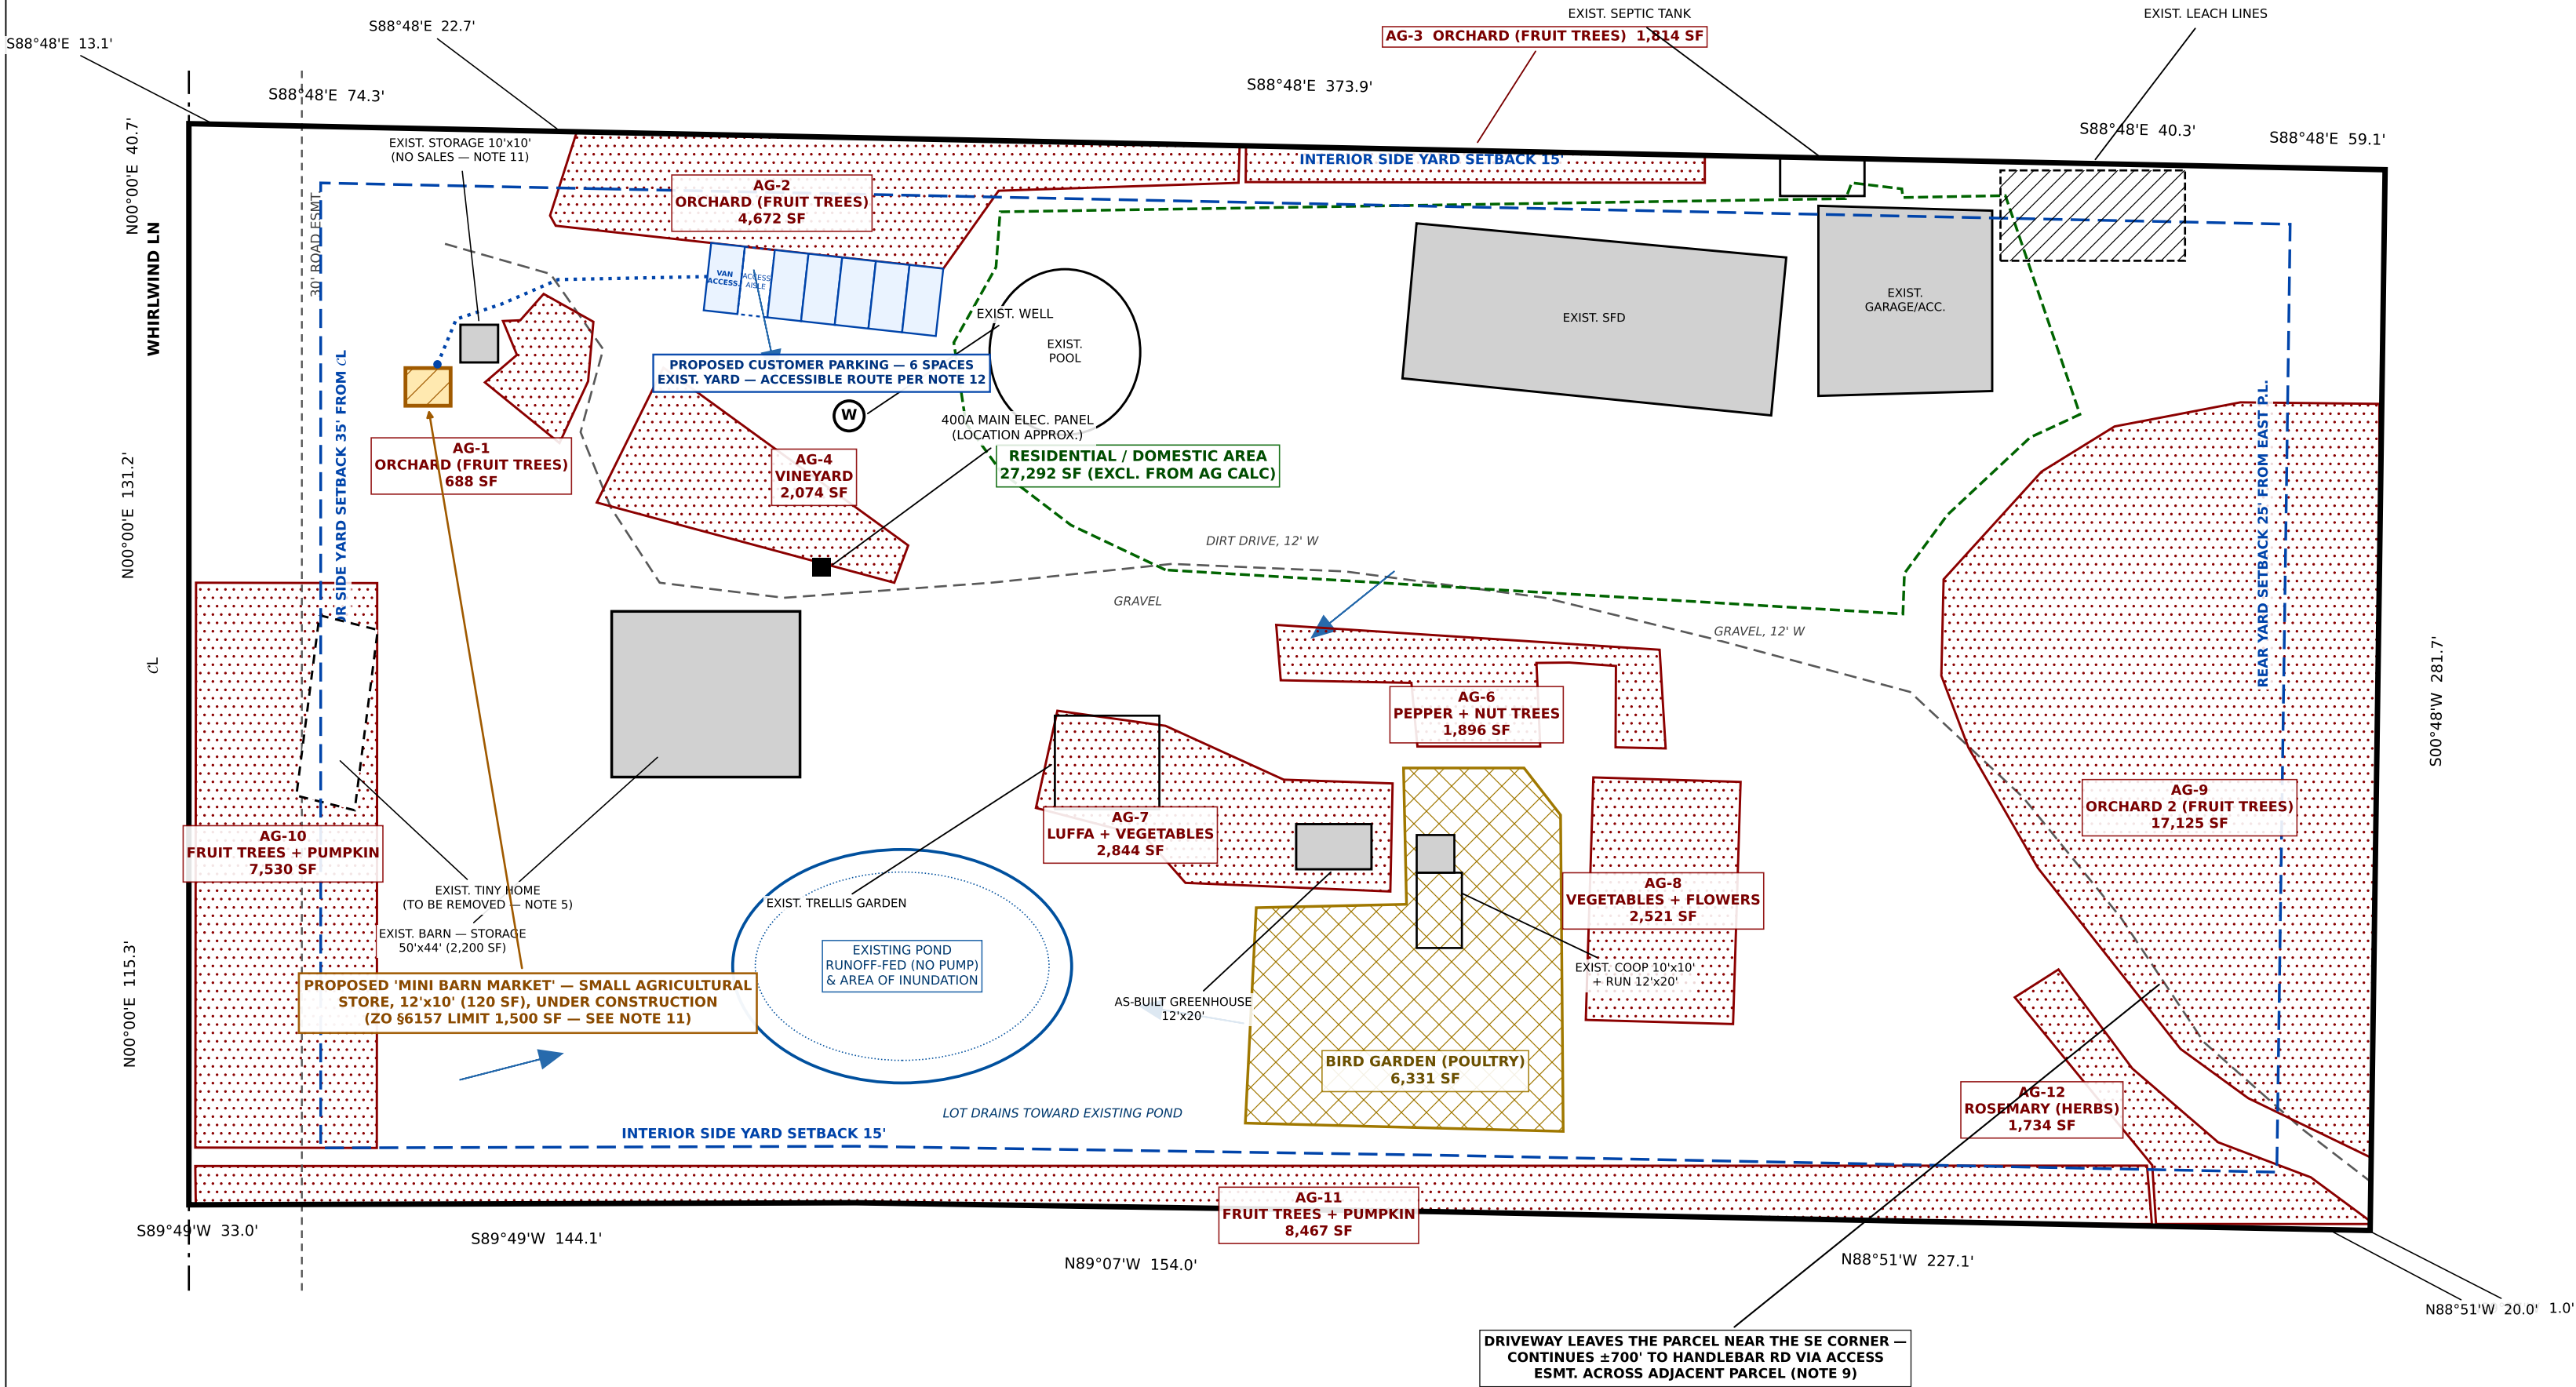

AGRICULTURAL USE CALCULATION

PER ZO §6157.a.2.b — GROSS BASIS

TOTAL GROSS AREA OF PREMISES 164,443 SF

b.i REQUIRED 50% SUITABLE / AVAILABLE 82,222 SF

PROVIDED (GROSS LESS RESIDENTIAL) 137,151 SF

= 83.4% OF GROSS PASSES

b.ii REQUIRED 25% IN ACTIVE AG USE 41,111 SF

CROP AREAS AG-1 THRU AG-12 51,365 SF

POULTRY (BIRD GARDEN) 6,331 SF

PROVIDED TOTAL ACTIVE AG USE 57,696 SF

= 35.1% OF GROSS PASSES

MARGIN OVER THE 25% REQUIREMENT +16,585 SF

BOTH ZO §6157.a.2.b THRESHOLDS ARE MET

NET AREA EXCL. ROAD ESMTS. (PDS 090 ITEM 12): 157,251 SF

ON THE NET BASIS AG USE IS 36.7% — MET EITHER WAY.

SMALL AGRICULTURAL STORE

COMPLIANCE — ZONING ORDINANCE §6157.a.2

(ZO UPDATE 102, PUBLISHED 3-26-2020)

§6157C COMMERCIAL AG MUST BE THE PRINCIPAL USE SEE b.i / b.ii

a PERMITTED IN A70 USE REGS. A70 — NO MIN. LOT SIZE

NO ZONING VERIFICATION PERMIT REQ'D PERMITTED BY RIGHT

b.i ≥50% OF GROSS SUITABLE/AVAILABLE 83.4% PROVIDED

b.ii ≥25% OF GROSS IN ACTIVE AG USE 35.1% PROVIDED

c OPERATED BY OWNER OR TENANT OWNER-OPERATED

d ONE STORE PER LEGAL LOT; NO EXIST. NONE EXISTING

AG STAND OR LARGE AG STORE

STORE ≤1,500 SF INCL. ROOFED DISPLAY 120 SF — COMPLIES

CONFORM TO §4810 SETBACKS STORE CLEARS ALL YARDS

PUBLIC AREAS TO COMM. BLDG. CODE + DEHQ SEE NOTE 11

f RETAIL ONLY WITH ON-SITE PRODUCE / EGGS; ACKNOWLEDGED

AG WEIGHTS & MEASURES REGS. APPLY

g ≤200 SF FOR OFF-SITE PRODUCTS TO BE DESIGNATED

h MINIMUM 6 PARKING SPACES 6 SHOWN, GRAVEL

DISABLED ACCESS PER CBC CH. 11B 1 VAN ACCESSIBLE

i HOURS 10 A.M. TO LEGAL SUNSET ACKNOWLEDGED

j ONE ON-PREMISE SIGN, MAX 4 SF ACKNOWLEDGED

k EVENTS PROHIBITED ACKNOWLEDGED

STORE AREA SUMMARY

STORE = NEW 'MINI BARN MARKET' BLDG 12'x10' 120 SF

OPEN ROOFED DISPLAY AREA 0 SF

TOTAL PER §6157.a.2.e — LIMIT 1,500 SF 120 SF

PARKING — ZO §6157.a.2.h

REQUIRED 6 SPACES

PROVIDED 6 SPACES

STANDARD 9' x 18' 5

VAN ACCESSIBLE 9' x 18' + 8' AISLE 1

SURFACE — GRAVEL (EXPRESSLY ALLOWED) EXISTING

THE STORE IS THE NEW 12'x10' MINI BARN MARKET BUILDING —

120 SF AGAINST A 1,500 SF LIMIT. THE ADJACENT 10'x10'

BUILDING IS STORAGE ONLY — NO SALES.

LEGEND

PROPOSED STORE ('MINI BARN MARKET' 12'x10')

PROPOSED CUSTOMER PARKING

AGRICULTURAL CROP AREA

POULTRY AREA (BIRD GARDEN)

RESIDENTIAL / DOMESTIC AREA

EXISTING STRUCTURE

STRUCTURE TO BE REMOVED

LEACH LINES

ROAD CENTERLINE

ROAD EASEMENT LINE

REQUIRED YARD SETBACK

DRIVEWAY CENTERLINE

DIRECTION OF LOT DRAINAGE

EXISTING WELL

STORMWATER (PDS 272)

NO GRADING OR CLEARING PROPOSED. NEW IMPERVIOUS AREA IS THE

12'x10' STORE BUILDING ONLY (120 SF) — UNDER PERMIT THRESHOLDS.

SD-B: RUNOFF DIRECTED TO PERVIOUS/LANDSCAPED AREAS.


SD-G: EXISTING NATURAL SWALES AND POND CONSERVED.

SD-H: VEGETATED BUFFER MAINTAINED AROUND EXISTING POND.

VICINITY MAP

(NOT TO SCALE)


HIGHLAND VALLEY RD

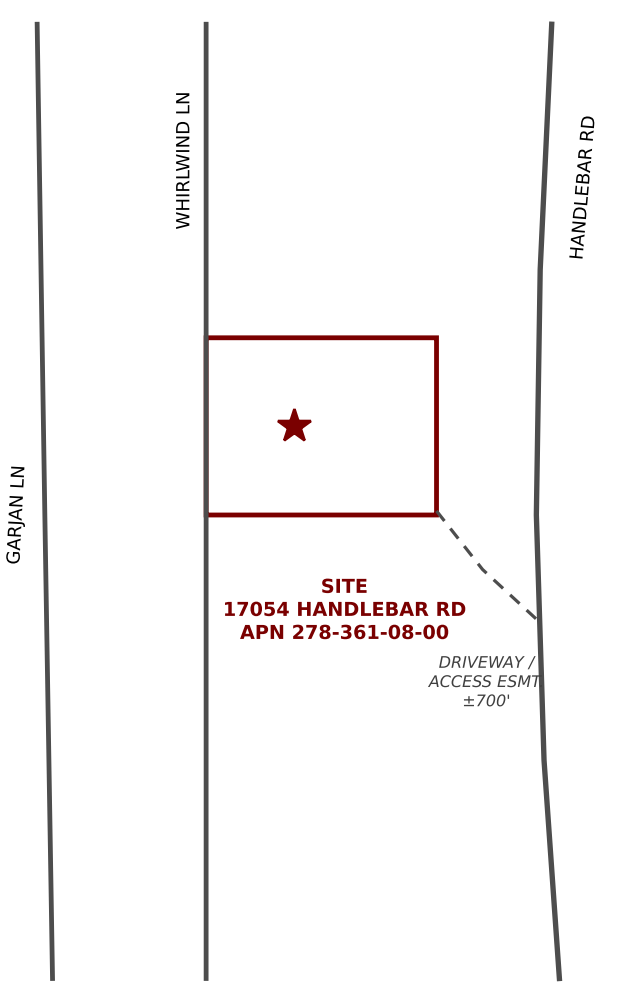

RAMONA, SAN DIEGO COUNTY, CALIFORNIA

N

GRAPHIC SCALE: 1" = 40'

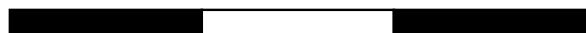

(FEET)