
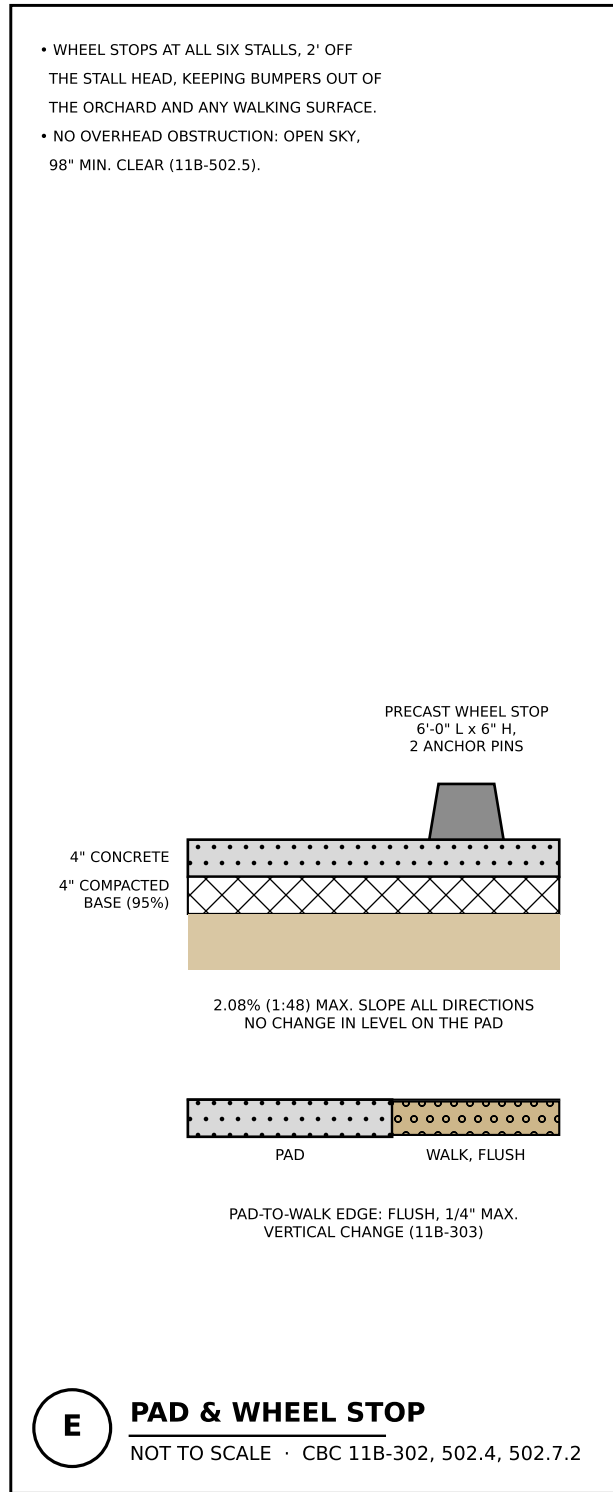
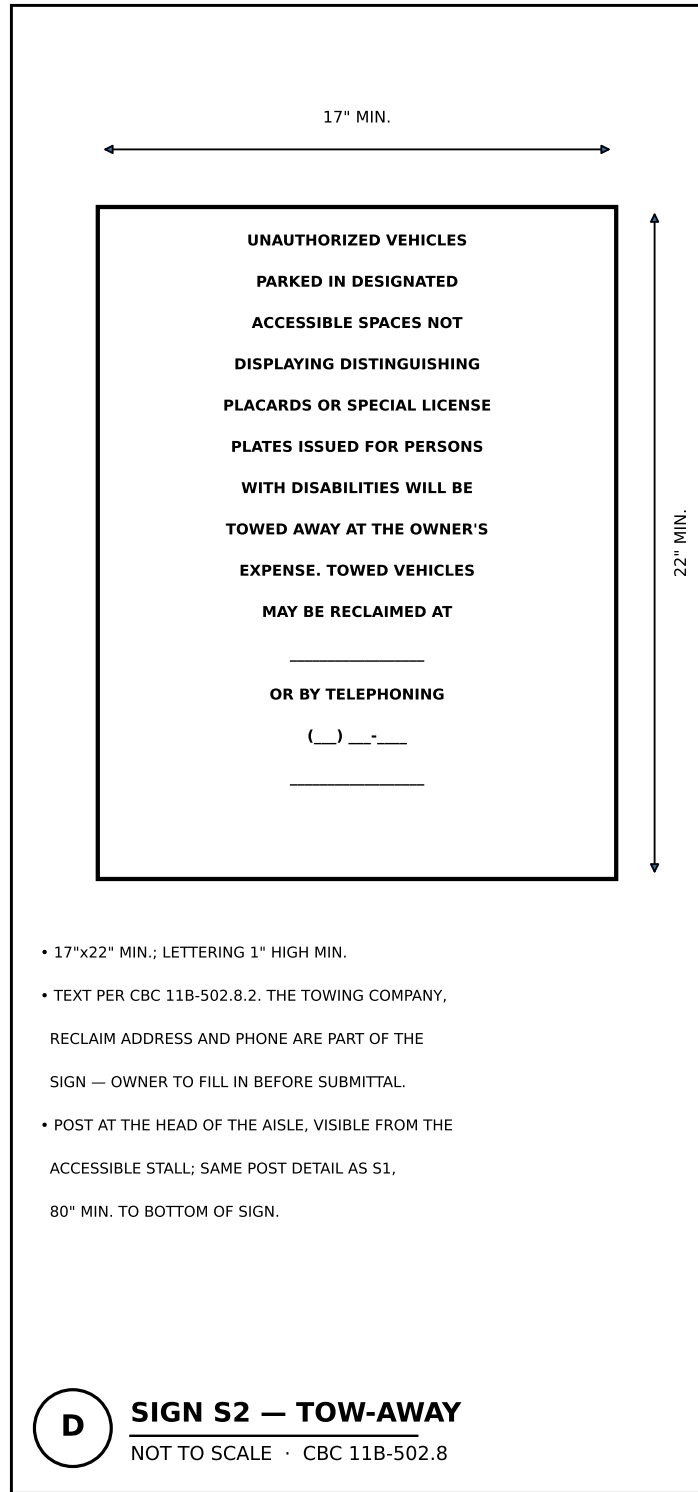
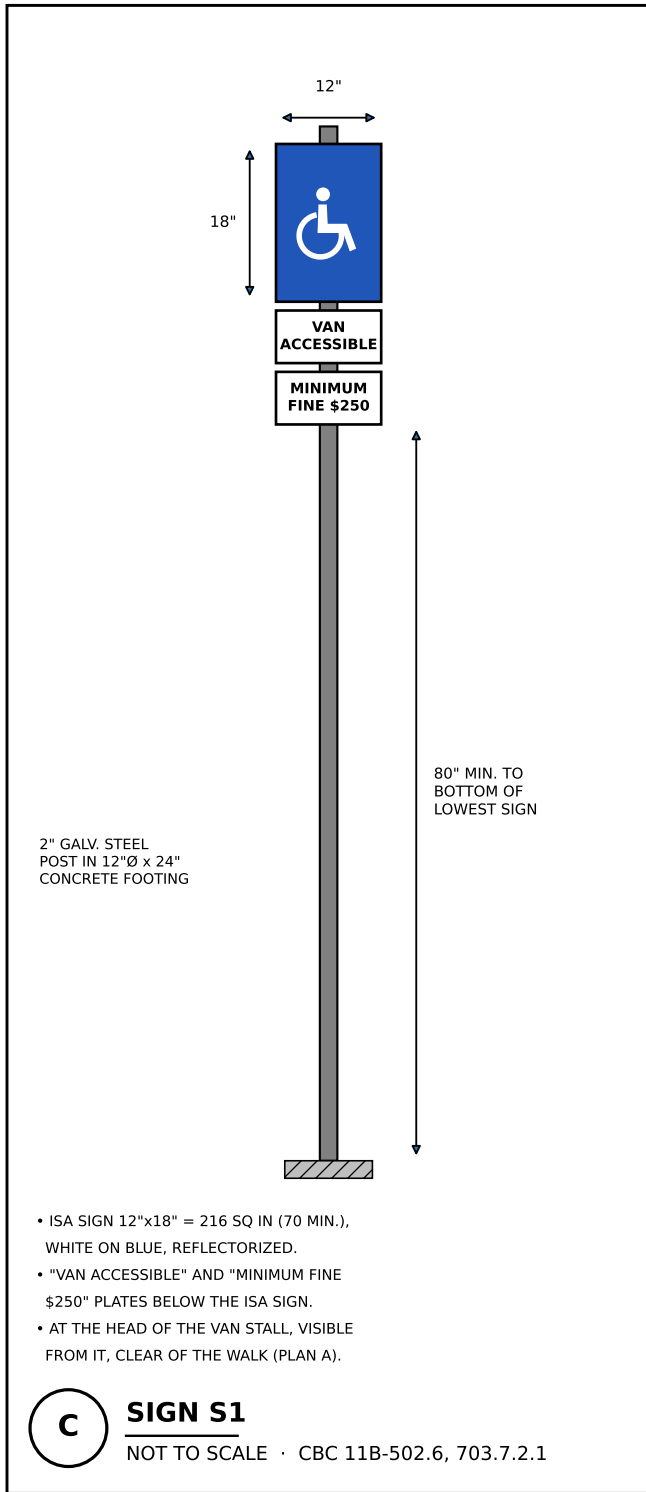
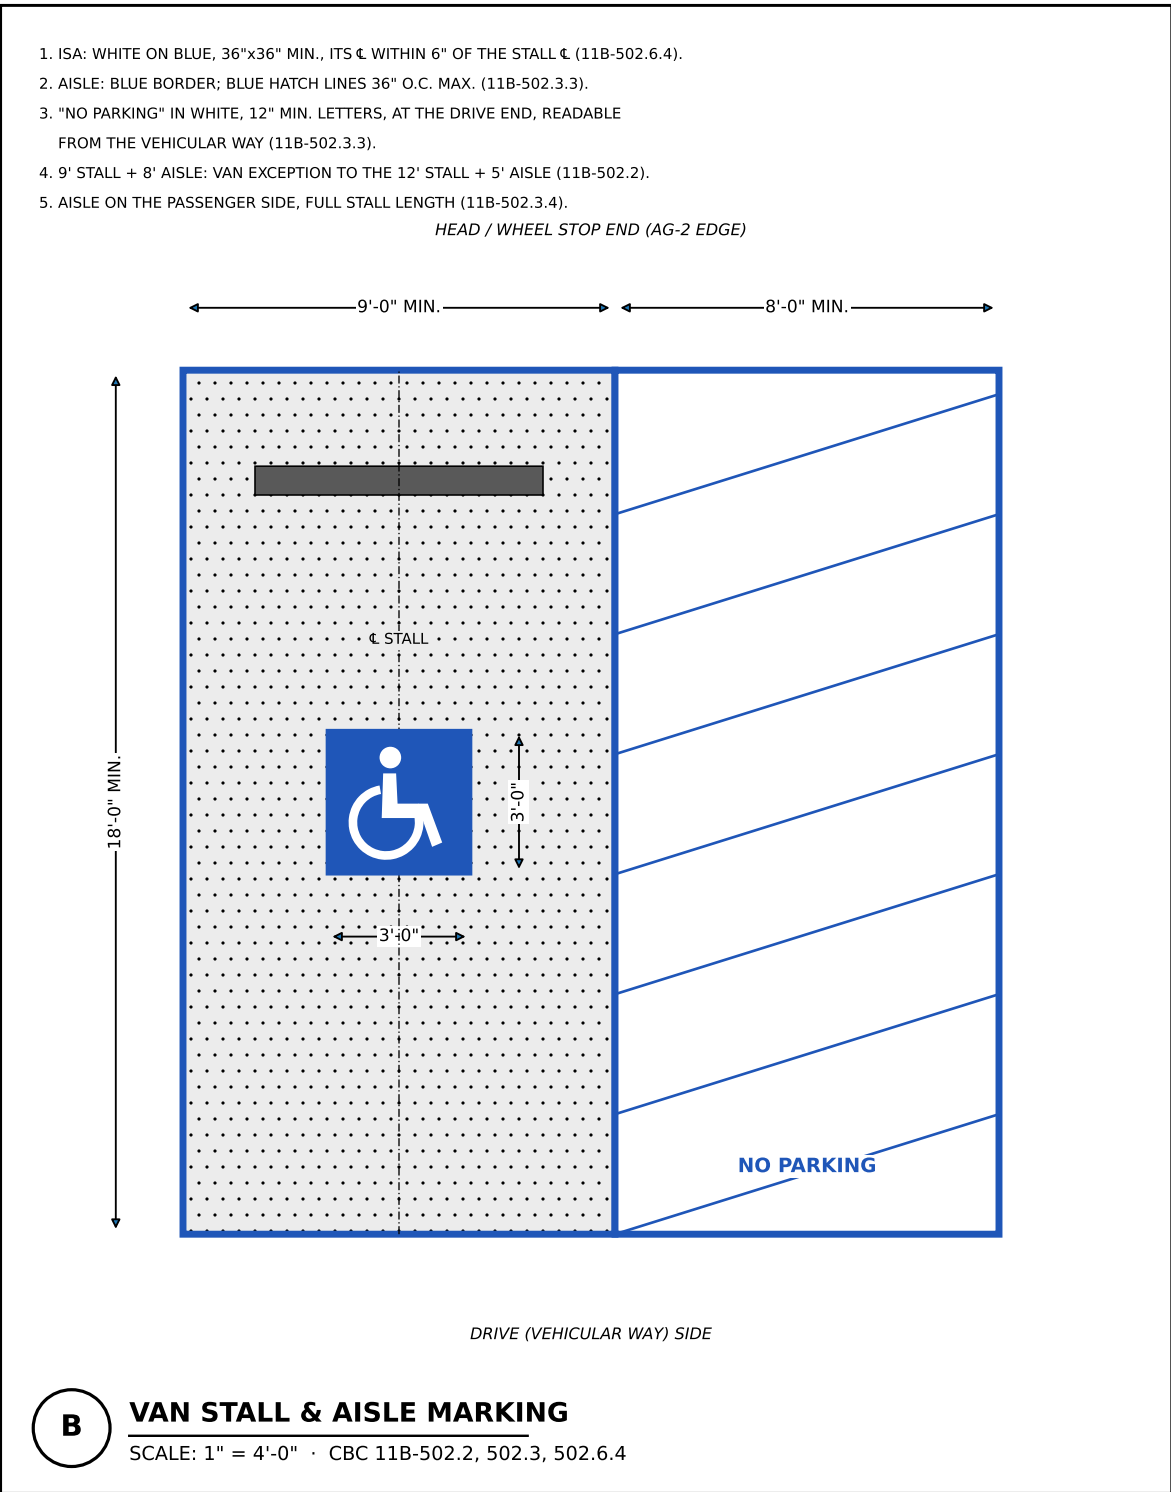
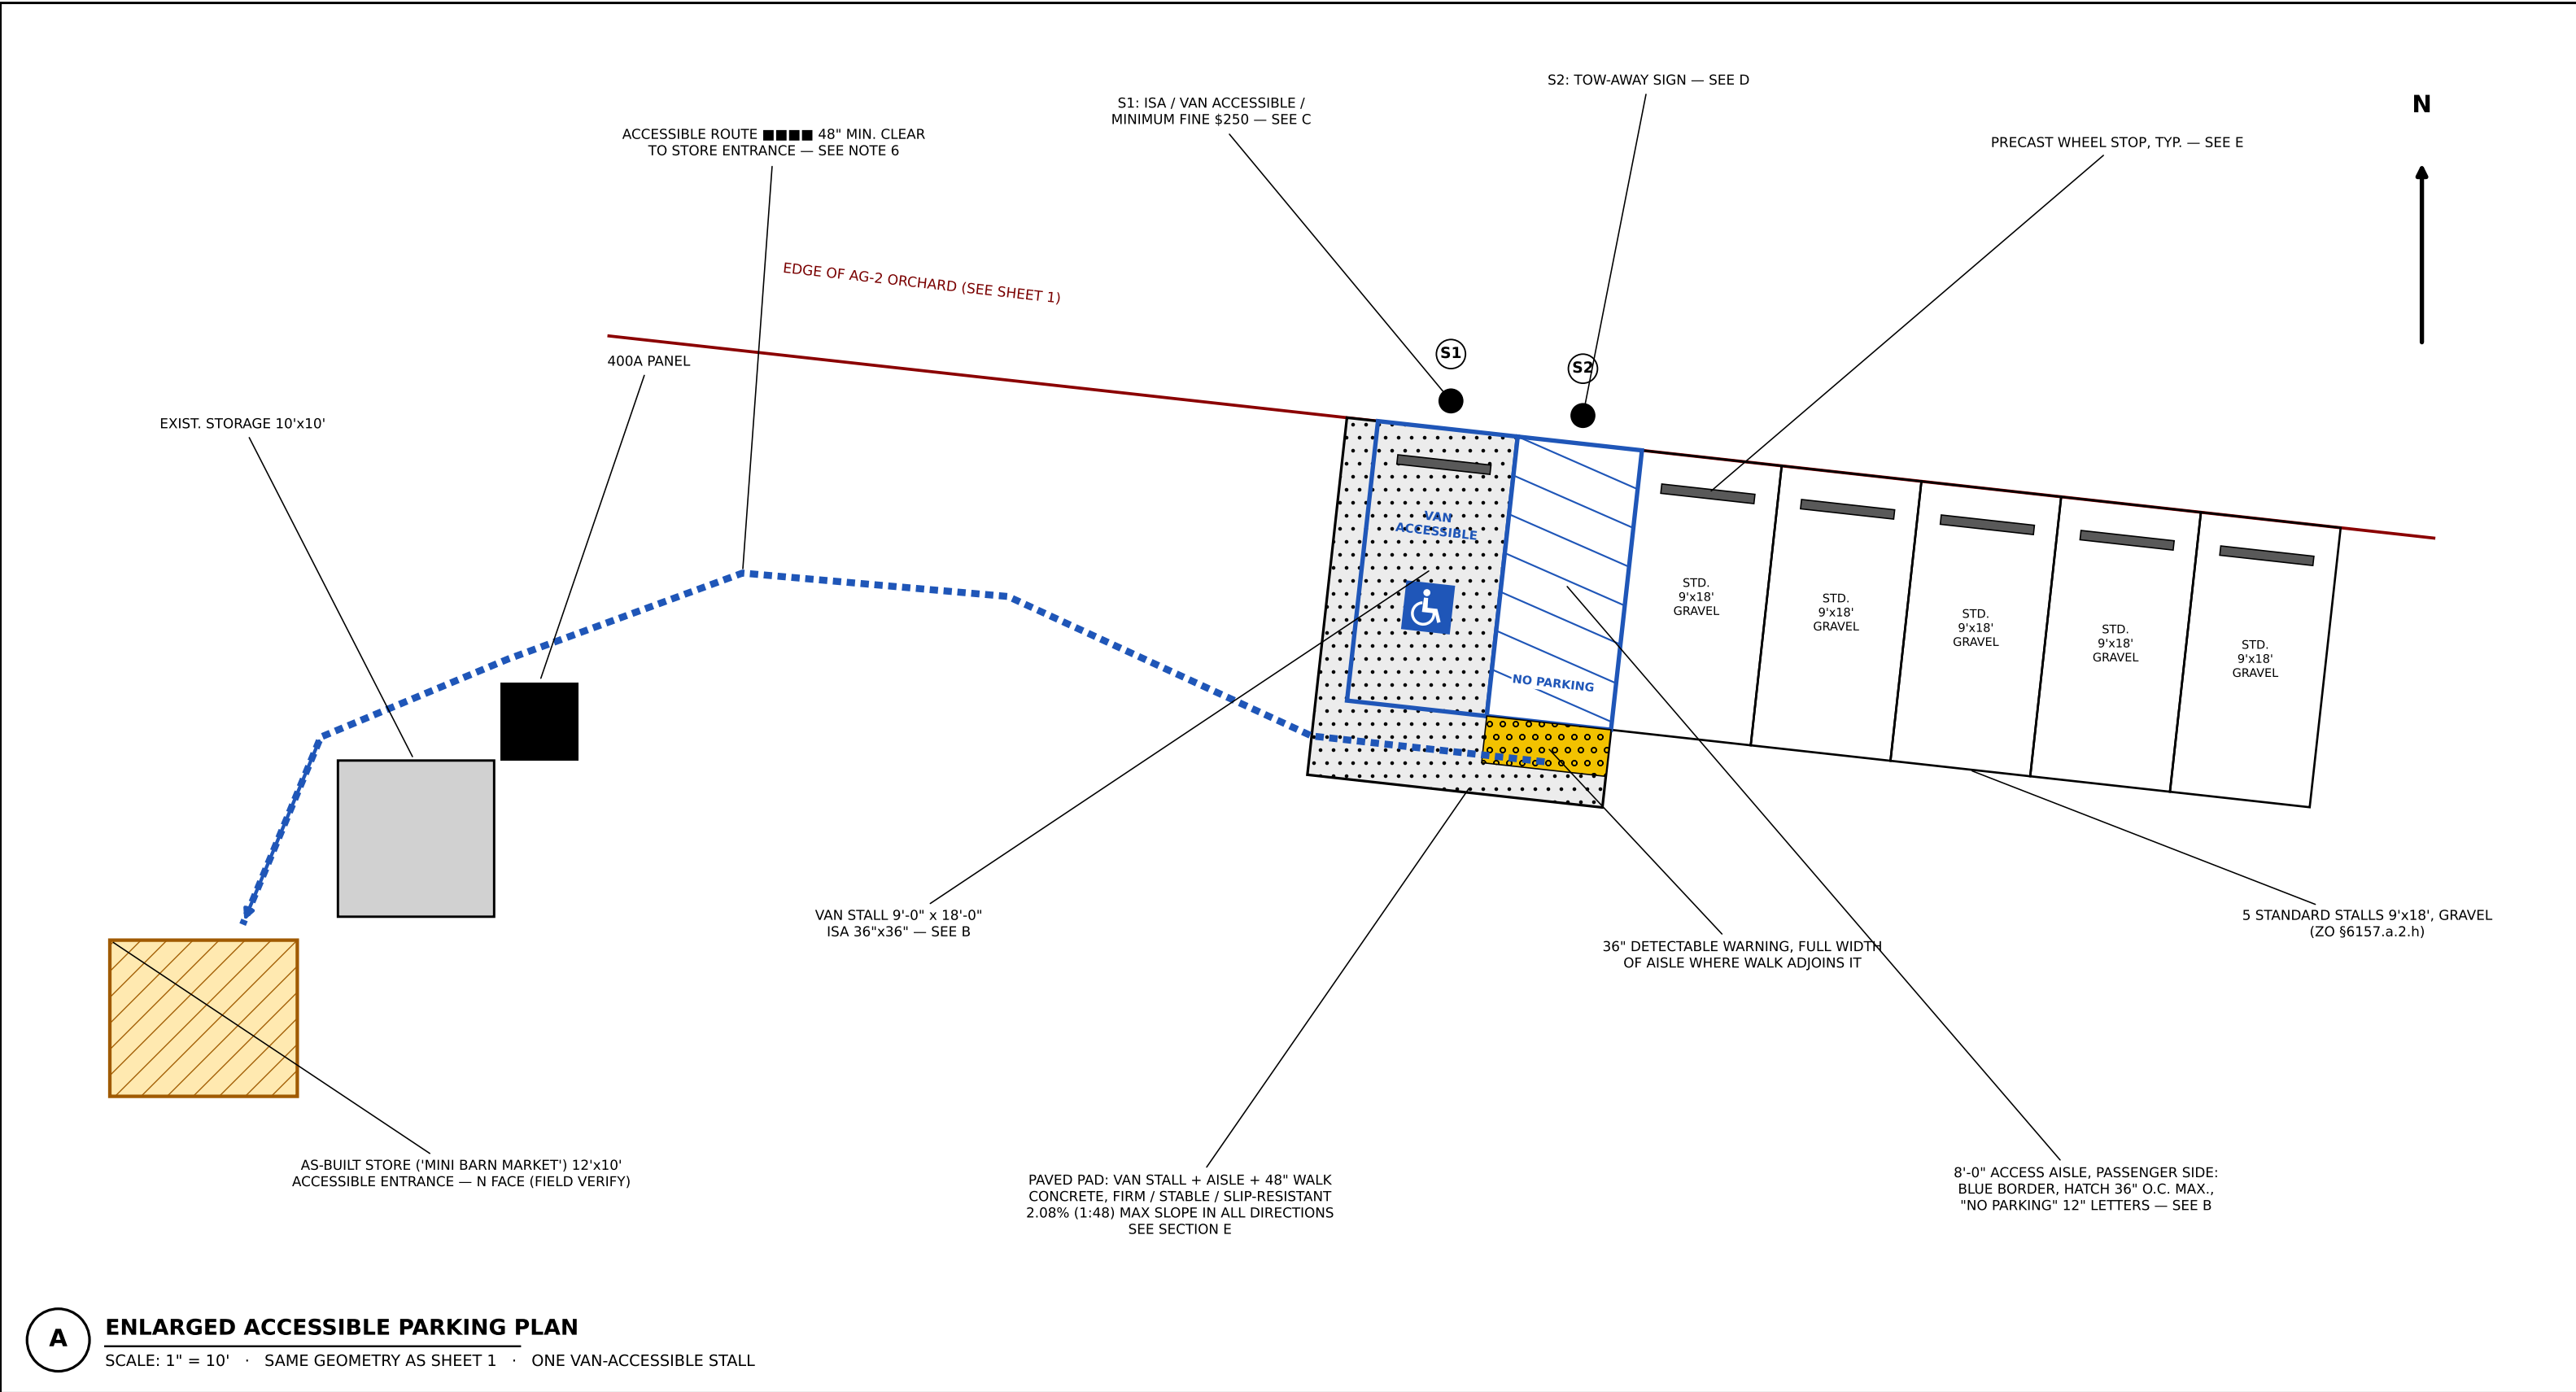
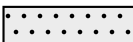


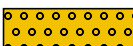

ACCESSIBLE PARKING DETAILS		
SMALL AGRICULTURAL STORE — ZO §6157.a.2.h / CBC CH. 11B		
17054 HANDLEBAR ROAD, RAMONA, CA 92065 · APN 278-361-08-00		
PARKING SCOPING		
TOTAL PARKING SPACES PROVIDED		6
ACCESSIBLE SPACES REQ'D (CBC TABLE 11B-208.2, 1-25 SPACES)		1
VAN-ACCESSIBLE REQ'D (11B-208.2.4, 1 PER 6 ACCESSIBLE)		1
ACCESSIBLE SPACES PROVIDED — VAN ACCESSIBLE		1
STANDARD SPACES, GRAVEL (ZO §6157.a.2.h)		5
ACCESSIBILITY NOTES		
1. ONE VAN-ACCESSIBLE STALL, 9'-0" x 18'-0" MIN., WITH AN 8'-0" MIN. ACCESS AISLE ON ITS PASSENGER SIDE, FULL STALL LENGTH (CBC 11B-502.2, 502.3). 2. STALL AND AISLE: CONCRETE, FIRM, STABLE AND SLIP-RESISTANT, NO CHANGES IN LEVEL, 2.08% (1:48) MAX. SLOPE IN ANY DIRECTION (11B-302, 11B-502.4). THE FIVE STANDARD STALLS STAY GRAVEL (ZO §6157.a.2.h). 3. SURFACE IDENTIFICATION PER DETAIL B: ISA 36"x36" WHITE ON BLUE; BLUE AISLE BORDER AND HATCH 36" O.C. MAX.; "NO PARKING" 12" MIN. LETTERS (11B-502.3.3, 11B-502.6.4). 4. SIGN S1 (DETAIL C): ISA SIGN 70 SQ IN MIN., REFLECTORIZED, WITH "VAN ACCESSIBLE" AND "MINIMUM FINE \$250" BELOW; 80" MIN. TO THE BOTTOM (11B-502.6, 11B-502.6.2, 11B-703.7.2.1). 5. SIGN S2 (DETAIL D): TOW-AWAY SIGN 17"x22" MIN., 1" MIN. LETTERING, TEXT AND TOWING CONTACT PER 11B-502.8, VISIBLE FROM THE ACCESSIBLE STALL. 6. ACCESSIBLE ROUTE ■■■■ FROM THE AISLE TO THE STORE ENTRANCE: 48" MIN. CLEAR, RUNNING SLOPE 5% MAX., CROSS SLOPE 2.08% MAX., FIRM, STABLE, SLIP-RESISTANT (CONCRETE OR STABILIZED DECOMPOSED GRANITE); CHANGES IN LEVEL 1/4" MAX. (11B-208.3, 11B-302, 11B-303, 11B-402, 11B-403). 7. THE ROUTE LEAVES THE AISLE AT ITS REAR AND PASSES ONLY BEHIND THE VAN STALL IT SERVES (11B-502.7.1). 8. 36" DEEP DETECTABLE WARNING (TRUNCATED DOMES, YELLOW) WHERE THE WALK ADJOINS THE AISLE WITHOUT A CURB (11B-247.1.2.5, 11B-705.1). 9. WHEEL STOPS AT ALL STALLS, SO NO VEHICLE OVERHANGS A WALKING SURFACE (11B-502.7.2). NO OVERHEAD OBSTRUCTIONS; 98" MIN. CLEAR (11B-502.5). 10. STORE ENTRANCE: ACCESSIBLE DOOR AND LANDING PER 11B-404 — CONFIRM WITH THE STORE BUILDING PERMIT (PUBLIC-ACCESSED AREAS).		
LEGEND		
	PAVED PAD — CONCRETE (VAN STALL, AISLE, WALK)	
	ACCESSIBLE ROUTE ■■■■ 48" MIN.	
	DETECTABLE WARNING, 36" DEEP	
	PRECAST WHEEL STOP	
	SIGN POST (S1, S2)	
AGRICULTURAL OPERATIONS & SMALL AGRICULTURAL STORE		
ACCESSIBLE PARKING DETAILS		
OWNER: CORY J. DZBINSKI & CARISSA ULTSCH		
17054 HANDLEBAR RD, RAMONA, CA 92065 · APN 278-361-08-00		
SCALE: AS NOTED	REV DATE	DESCRIPTION
DETAILS V1 · DRAFT FOR OWNER REVIEW	V1	9/15/2026 FIRST ISSUE
SHEET 2 OF 2		