

AGRICULTURAL OPERATIONS & SMALL AGRICULTURAL STORE PLOT PLAN

17054 HANDLEBAR ROAD, RAMONA, CA 92065

APN 278-361-08-00 · ZONE A70 (LIMITED AGRICULTURE)

ZONING BOX: A70 / L / 2AC / C / G / C / C

LEGAL: PARCEL 1 OF PARCEL MAP 05062 (FILE NO. 69370)

GROSS AREA: 164,443 SF (3.78 AC) · NET AREA: 157,251 SF (3.61 AC)

OWNER: CORY J. DZBINSKI & CARISSA ULTSCH

17054 HANDLEBAR RD, RAMONA, CA 92065

farmhousegetaways@gmail.com

PREPARED BY: OWNER

AGRICULTURAL USE SUMMARY

ZONE	USE / CROP	AREA
AG-1	ORCHARD (FRUIT TREES)	656 SF
AG-2	ORCHARD (FRUIT TREES)	4,100 SF
AG-3	ORCHARD (FRUIT TREES)	1,064 SF
AG-4	VINEYARD	2,012 SF
AG-6	PEPPER + NUT TREES	1,883 SF
AG-7	LUFFA + VEGETABLES	2,826 SF
AG-8	VEGETABLES + FLOWERS	2,518 SF
AG-9	ORCHARD 2 (FRUIT TREES)	16,690 SF
AG-10	FRUIT TREES + PUMPKIN	7,223 SF
AG-11	FRUIT TREES + PUMPKIN	6,118 SF
AG-12	ROSEMARY (HERBS)	1,659 SF
BG	BIRD GARDEN (POULTRY)	6,315 SF

TOTAL ACTIVE AGRICULTURAL AREA 53,063 SF

= 32.3% OF GROSS (ZO 6157.a.2.b.ii REQ.: 25% = 41,111 SF)

AG-5 NOT USED — NUMBERING RETAINED PER OWNER FIELD NOTES. AREAS ARE CLIPPED TO THE PARCEL BOUNDARY (NOTE 2).

STRUCTURE SUMMARY

STRUCTURE / USE	STATUS	FOOTPRINT
SMALL AGRICULTURAL STORE (IN BARN)	PROPOSED	1,500 SF
CUSTOMER PARKING, 6 SPACES	PROPOSED	1,116 SF
BARN ('MINI BARN MARKET')	EXISTING	3,400 SF
SFD — RESIDENCE (4BR/2BA, 2,724 SF LIV.)	EXISTING	4,110 SF
GARAGE / ACCESSORY BLDG	EXISTING	2,270 SF
SHED (NW) — STORAGE	EXISTING	415 SF
SHED (NE) — STORAGE	EXISTING	165 SF
CANOPY (NE)	EXISTING	285 SF
TRELLIS GARDEN (OPEN)	EXISTING	690 SF
GREENHOUSE 12'x20'	AS-BUILT	240 SF
POULTRY COOP 10'x10'	EXISTING	100 SF
POULTRY RUN 12'x20'	EXISTING	240 SF
POOL	EXISTING	1,380 SF
TINY HOME (W)	TO BE REMOVED	765 SF
FOOTPRINTS AERIAL-DERIVED, APPROXIMATE (NOTE 2).		

NOTES

- BOUNDARY: SHOWN PER COUNTY GIS PARCEL POLYGON (164,443 SF). THE ASSESSOR'S MAP (BK 278 PG 36) SHOWS THE RECORD PARCEL AS 550.50' x 285.58' = 157,212 SF (3.61 AC). THE TWO DIFFER: RECORDED PM 05062 GOVERNS AND IS NOT YET OBTAINED. THE AG-USE TESTS ARE MET ON EITHER BASIS.
- AG AREAS AND STRUCTURE FOOTPRINTS AERIAL-DERIVED AND FIELD-CORROBORATED; CROP AREAS ARE CLIPPED TO THE PARCEL AND TABULATED AS CLIPPED. OWNER FIELD VERIFICATION CONTINUING. AG-9 LEGS MEASURED 200'/130'/190'; W AND N CURVE OUT. (d): A LOT FRONTING A PRIVATE EASEMENT UNDER 40' WIDE TAKES A 40' FRONT YARD FROM 4' — APPLIED HERE TO WHIRLWIND LN. FRONTAGE TO BE CONFIRMED WITH PDS.
- NO GRADING AND NO NEW BUILDING PROPOSED. THIS PLAN DOCUMENTS EXISTING AG OPERATIONS AND A PROPOSED SMALL AGRICULTURAL STORE (ZO 6157).
- SETBACKS PER THE PARCEL ZONING BOX, DESIGNATOR C, ZO 64810 SCHEDULE C: FRONT 60' FROM 4', INTERIOR SIDE 15', EXTERIOR SIDE 35' FROM 4', REAR 25'. FOOTNOTE (d): A LOT FRONTING A PRIVATE EASEMENT UNDER 40' WIDE TAKES A 40' FRONT YARD FROM 4' — APPLIED HERE TO WHIRLWIND LN. FRONTAGE TO BE CONFIRMED WITH PDS.
- EXISTING STRUCTURES WITHIN A REQUIRED YARD AS MAPPED: GARAGE/ACCESSORY 12.7'; NE CANOPY 0.9' AND NE SHED AT THE NORTH LINE (15' INTERIOR SIDE REQ'D); TINY HOME 13.5' FROM WHIRLWIND 4' (40' REQ'D). ALL EXISTING — NO NEW WORK PROPOSED IN ANY YARD. POSITIONS AERIAL/GIS-DERIVED AND APPROXIMATE; CONFIRM EXISTING / LEGAL-NONCONFORMING STATUS WITH PDS. A SURVEYOR'S SETBACK CERTIFICATE MAY BE REQUIRED. THE PROPOSED STORE CLEARS EVERY REQUIRED YARD.
- POOL IS AN EXISTING IRRIGATION SOURCE (PUMP) AND THE AREA OF INUNDATION: LOT DRAINS TO POND, WELL, SEPTIC AND LEACH LINES PER OWNER, APPROXIMATE.
- GREENHOUSE SHOWN AS-BUILT (UNPERMITTED); MAY QUALIFY FOR THE AGRICULTURAL BUILDING EXEMPTION — CONFIRM WITH PDS. ELECTRICAL: 400A MAIN PANEL NE OF BARN.
- DRIVEWAY RUNS E-W FROM HANDLEBAR RD; GRAVEL BOTH ENDS, DIRT MID-SEGMENT PAST THE RESIDENCE, 12' WIDE; SLOPE 2% DRAINING WEST TOWARD THE POND.
- WHIRLWIND LN: 30' ROAD ESMT. ALONG THE WEST BOUNDARY, 4' ASSUMED AT MID-ESMT. HANDLEBAR RD IS A PRIVATE ROAD ESMT. CROSSING THE EAST PORTION, 4' SHOWN; ASSESSOR'S MAP DIMENSIONS THAT CORRIDOR AS 30'. BOTH WIDTHS AND CENTERLINES TO BE VERIFIED AGAINST PM 05062. IF PDS DEEMS HANDLEBAR RD THE FRONTAGE, A 40' FRONT YARD FROM ITS 4' WOULD APPLY.
- NO NEW OR MODIFIED LANDSCAPE AREA PROPOSED (PDS 090 ITEM 16). EXISTING AG AND PERIMETER FENCING ONLY; HEIGHTS TO BE FIELD-VERIFIED AND ADDED PRIOR TO SUBMITTAL. NO NEW FENCES, WALLS OR GATES PROPOSED.
- ZO 6157.a.2.e LIMITS THE STORE TO 1,500 SF TOTAL INCLUDING OPEN ROOFED DISPLAY. IT IS SHOWN AS A DEMISED 1,500 SF PORTION OF THE EXISTING BARN; NO OTHER STRUCTURE WILL BE USED FOR ON-SITE SALES. PUBLIC AREAS TO BE PERMITTED AND BUILT TO THE COMMERCIAL BUILDING CODE AND DEMO REQUIREMENTS. CONFIRM WITH PDS THAT A DEMISED PORTION OF A LARGER BUILDING SATISFIES 6157.a.2.e.
- ACCESSIBLE STALL, AISLE AND THE ROUTE TO THE STORE ENTRANCE TO BE A STABLE, FIRM, SLIP-RESISTANT SURFACE PER CBC CH. 11B AND 6157.a.2.h.

AGRICULTURAL OPERATIONS & SMALL AGRICULTURAL STORE

PLOT PLAN — EXISTING CONDITIONS & PROPOSED STORE

17054 HANDLEBAR RD, RAMONA, CA 92065

APN 278-361-08-00 · ZONE A70


SCALE: 1" = 40'

DATE: 8/19/2026

SHEET 1 OF 1

REV DATE DESCRIPTION

- | | | |
|---|-----------|-------------------------------------|
| 4 | 8/06/2026 | BASE SHEET |
| 5 | 8/06/2026 | SETBACK LINES ADDED |
| 6 | 8/19/2026 | FARM STORE ADDED |
| 7 | 8/19/2026 | SETBACKS & AREAS PER TRUE LOT LINES |

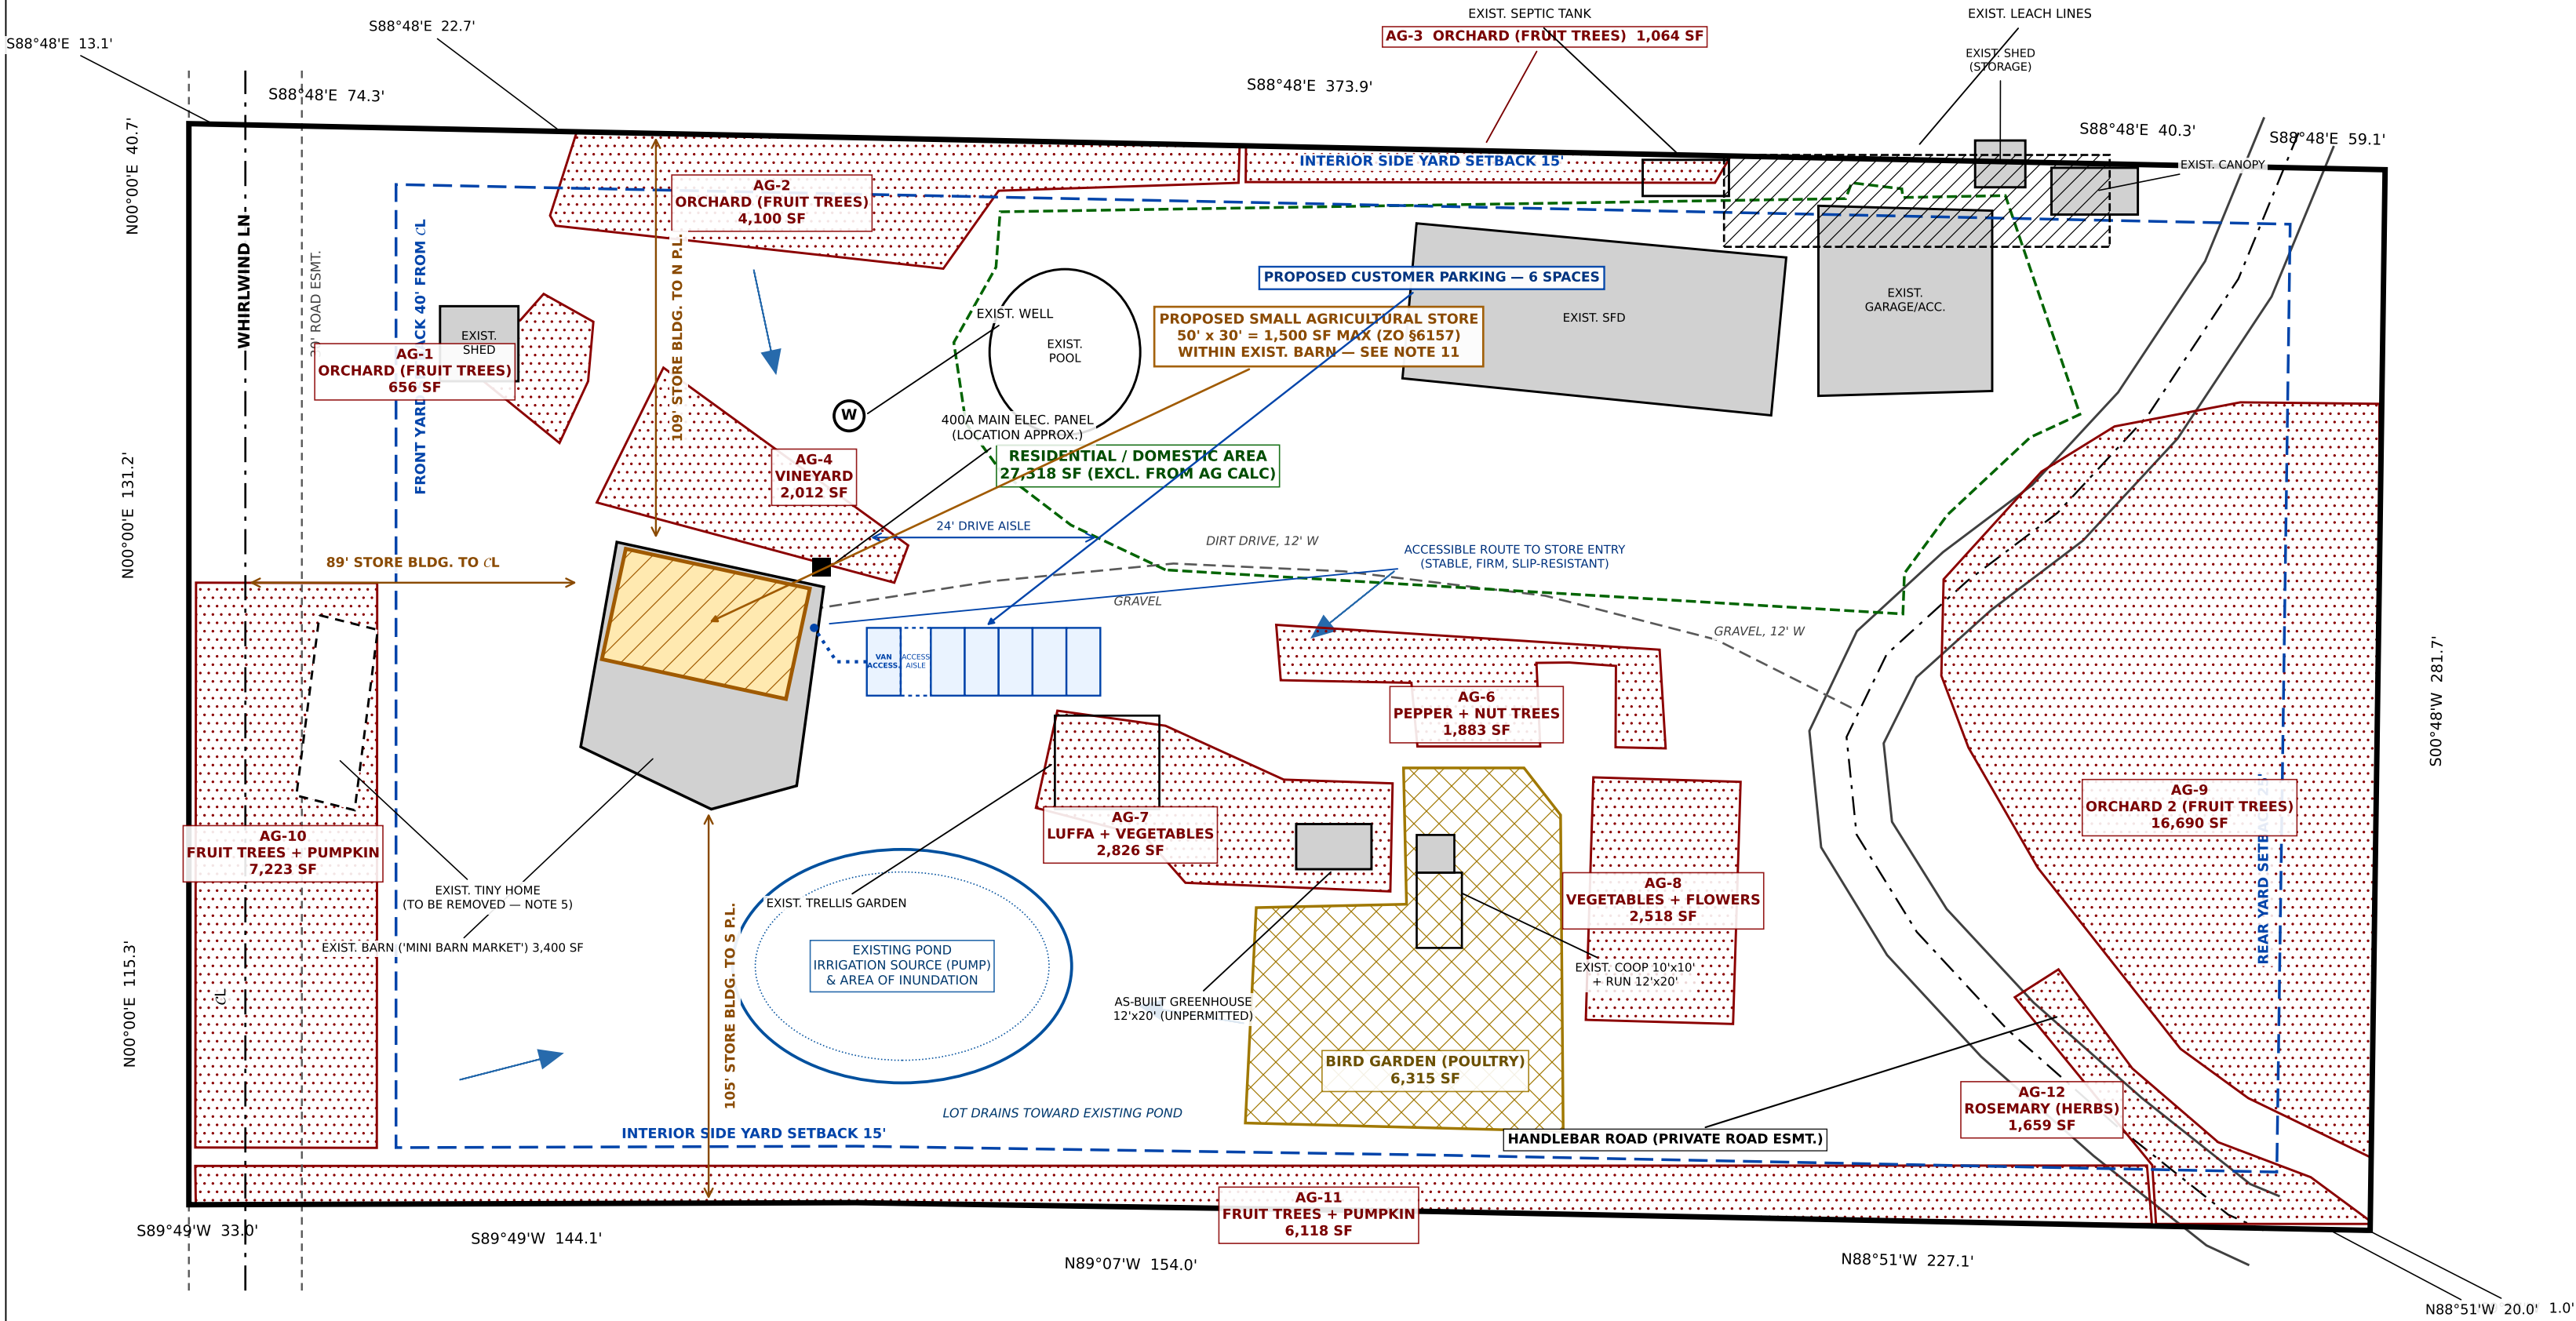

AGRICULTURAL USE CALCULATION

PER ZO 6157.a.2.b — GROSS BASIS

TOTAL GROSS AREA OF PREMISES	164,443 SF
b.i REQUIRED 50% SUITABLE / AVAILABLE	82,222 SF
PROVIDED (GROSS LESS RESIDENTIAL)	137,125 SF
= 83.4% OF GROSS	PASSES
b.ii REQUIRED 25% IN ACTIVE AG USE	41,111 SF
CROP AREAS AG-1 THRU AG-12	46,749 SF
POULTRY (BIRD GARDEN)	6,315 SF
PROVIDED TOTAL ACTIVE AG USE	53,063 SF
= 32.3% OF GROSS	PASSES
MARGIN OVER THE 25% REQUIREMENT	+11,952 SF

BOTH ZO 6157.a.2.b THRESHOLDS ARE MET

ON THE RECORD PARCEL (157,212 SF — SEE BOUNDARY NOTE)

AG USE IS 33.8% — THE TESTS ARE MET ON EITHER BASIS.

NET AREA EXCL. ROAD ESMTS. (PDS 090 ITEM 12): 157,251 SF

SMALL AGRICULTURAL STORE COMPLIANCE — ZONING ORDINANCE 6157.a.2 (ZO UPDATE 102, PUBLISHED 3-26-2020)

6157COMMERCIAL AG MUST BE THE PRINCIPAL USE	SEE b.i / b.ii
a PERMITTED IN A70 USE REGS.	A70 — NO MIN. LOT SIZE
NO ZONING VERIFICATION PERMIT REQ'D	PERMITTED BY RIGHT
b.i ≥50% OF GROSS SUITABLE/AVAILABLE	83.4% PROVIDED
b.ii ≥25% OF GROSS IN ACTIVE AG USE	32.3% PROVIDED
c OPERATED BY OWNER OR TENANT	OWNER-OPERATED
d ONE STORE PER LEGAL LOT; NO EXIST. AG STAND OR LARGE AG STORE	NONE EXISTING
e STORE ≤1,500 SF INCL. ROOFED DISPLAY CONFORM TO §4810 SETBACKS	1,500 SF SHOWN
PUBLIC AREAS TO COMM. BLDG. CODE + DEMO	STORE CLEARS ALL YARDS
f RETAIL ONLY WITH ON-SITE PRODUCE / EGGS; AG WEIGHTS & MEASURES REGS. APPLY	SEE NOTE 11
g ≤200 SF FOR OFF-SITE PRODUCTS	ACKNOWLEDGED
h MINIMUM 6 PARKING SPACES	TO BE DESIGNATED
DISABLED ACCESS PER CBC CH. 11B	6 SHOWN, GRAVEL
i HOURS 10 A.M. TO LEGAL SUNSET	1 VAN ACCESSIBLE
j ONE ON-PREMISE SIGN, MAX 4 SF	ACKNOWLEDGED
k EVENTS PROHIBITED	ACKNOWLEDGED

STORE AREA SUMMARY

PROPOSED STORE FLOOR AREA	1,500 SF
OF WHICH OFF-SITE PRODUCTS (MAX)	200 SF
OPEN ROOFED DISPLAY AREA	0 SF
TOTAL PER 6157.a.2.e — LIMIT 1,500 SF	1,500 SF

PARKING — ZO 6157.a.2.h

REQUIRED	6 SPACES
PROVIDED	6 SPACES
STANDARD 9' x 18'	5
VAN ACCESSIBLE 9' x 18' + 8' AISLE	1
SURFACE — GRAVEL (EXPRESSLY ALLOWED)	PROPOSED

OUTSTANDING — CONFIRM WITH PDS ZONING

6157.a.2.e LIMITS THE STORE TO 1,500 SF. THE EXISTING BARN IS LARGER. CONFIRM A DEMISED ≤1,500 SF PORTION SATISFIES IT, OR SITE THE STORE IN A SEPARATE ≤1,500 SF STRUCTURE.

LEGEND

	PROPOSED SMALL AGRICULTURAL STORE
	PROPOSED CUSTOMER PARKING
	AGRICULTURAL CROP AREA
	POULTRY AREA (BIRD GARDEN)
	RESIDENTIAL / DOMESTIC AREA
	EXISTING STRUCTURE
	STRUCTURE TO BE REMOVED
	LEACH LINES
	ROAD CENTERLINE
	ROAD EASEMENT LINE
	REQUIRED YARD SETBACK
	DRIVEWAY CENTERLINE
	DIRECTION OF LOT DRAINAGE
	EXISTING WELL


STORMWATER (PDS 272)

PROPOSED LAND DISTURBANCE: 0 SF. NO GRADING, CLEARING OR CONSTRUCTION PROPOSED; NO NEW OR REPLACED IMPERVIOUS AREA. SD-B: RUNOFF DIRECTED TO PERVIOUS/LANDSCAPED AREAS. SD-G: EXISTING NATURAL SWALES AND POND CONSERVED. SD-H: VEGETATED BUFFER MAINTAINED AROUND EXISTING POND.

VICINITY MAP

(NOT TO SCALE)

HIGHLAND VALLEY RD

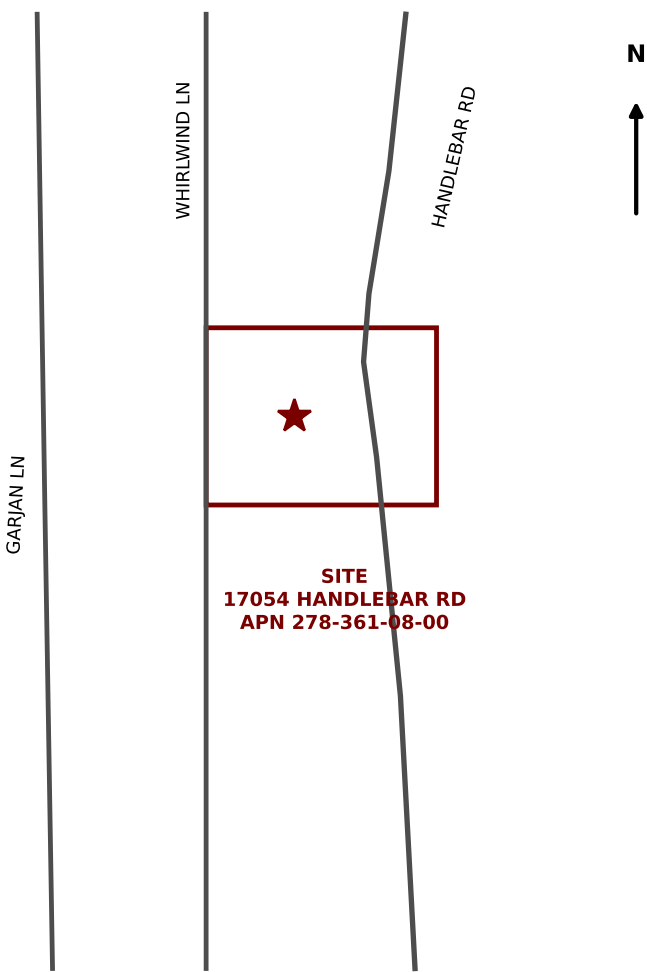

RAMONA, SAN DIEGO COUNTY, CALIFORNIA

GRAPHIC SCALE: 1" = 40'

